

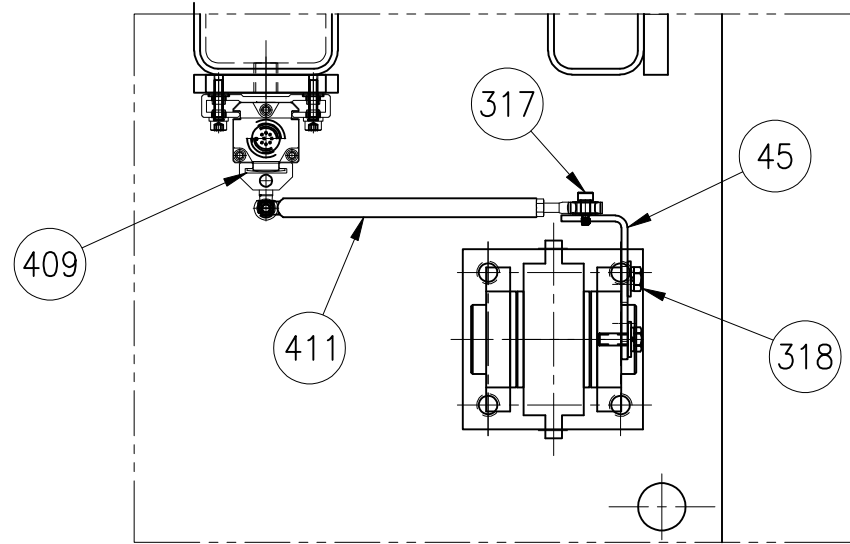



NOTE:  
WHEN ACCUMULATOR IS FULLY ASSEMBLED  
CARRIAGE MUST FALL TO THE BOTTOM  
BY ITS OWN WEIGHT  
SHOP NOTE:  
LOCATE AND MOUNT ITEM #403 & #404  
(LIMIT SWITCHES/LEVERS)

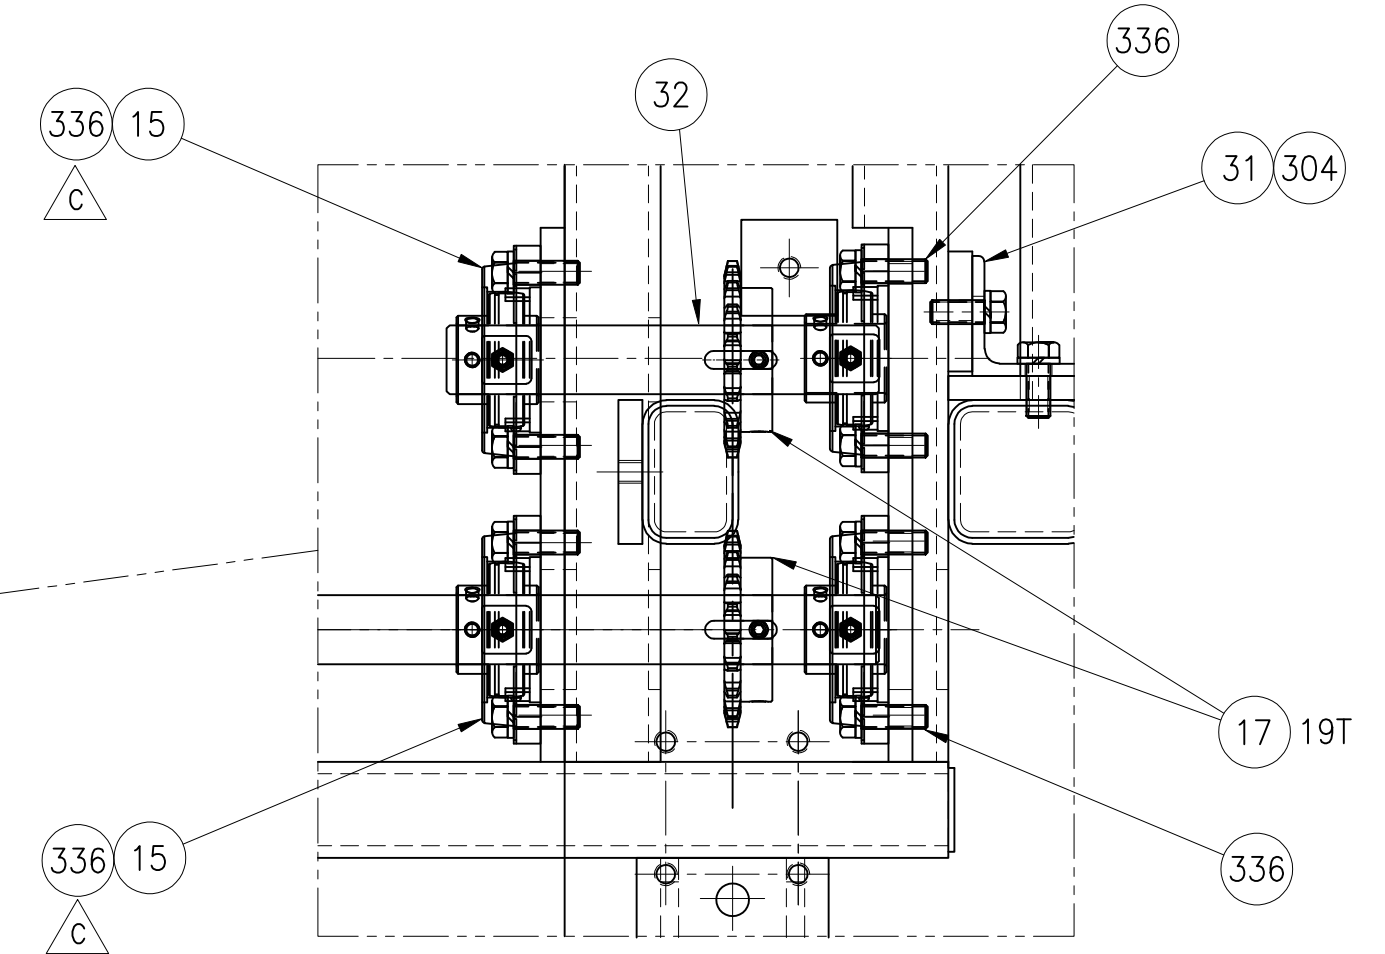

DETAIL VIEW F  
SCALE: 6" = 1'-0"

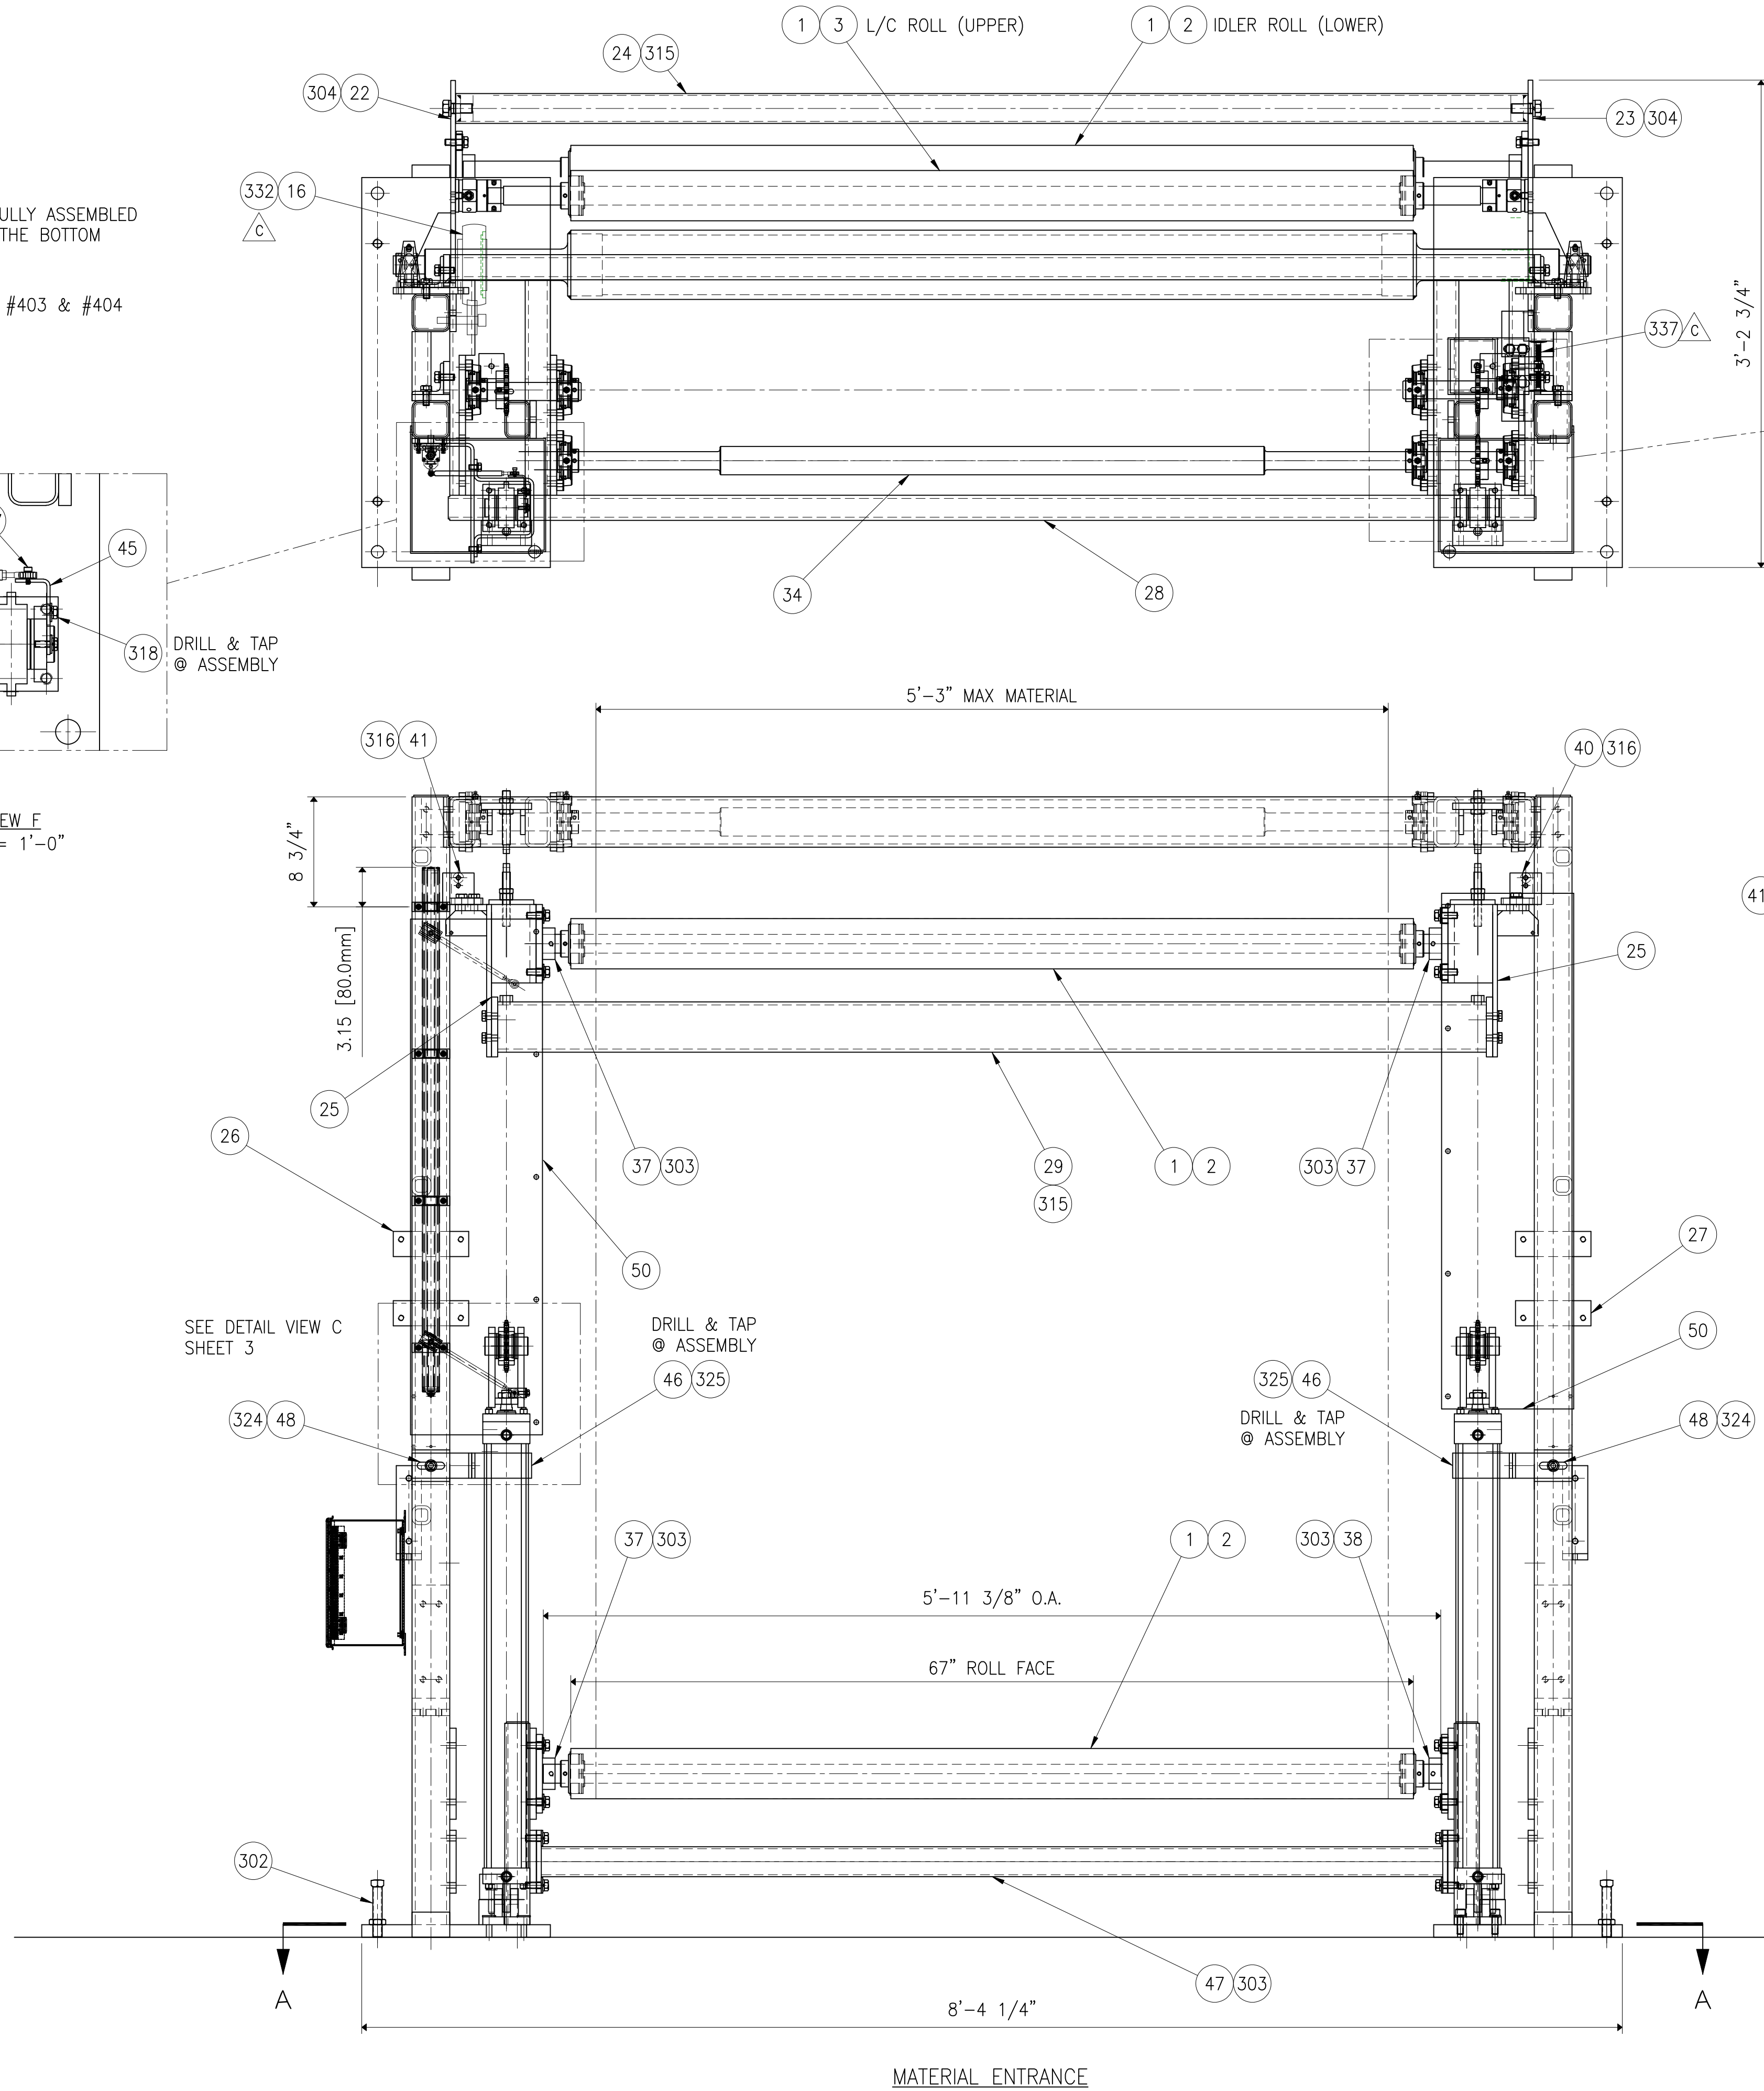

DETAIL VIEW B  
SCALE: 6" = 1'-0"

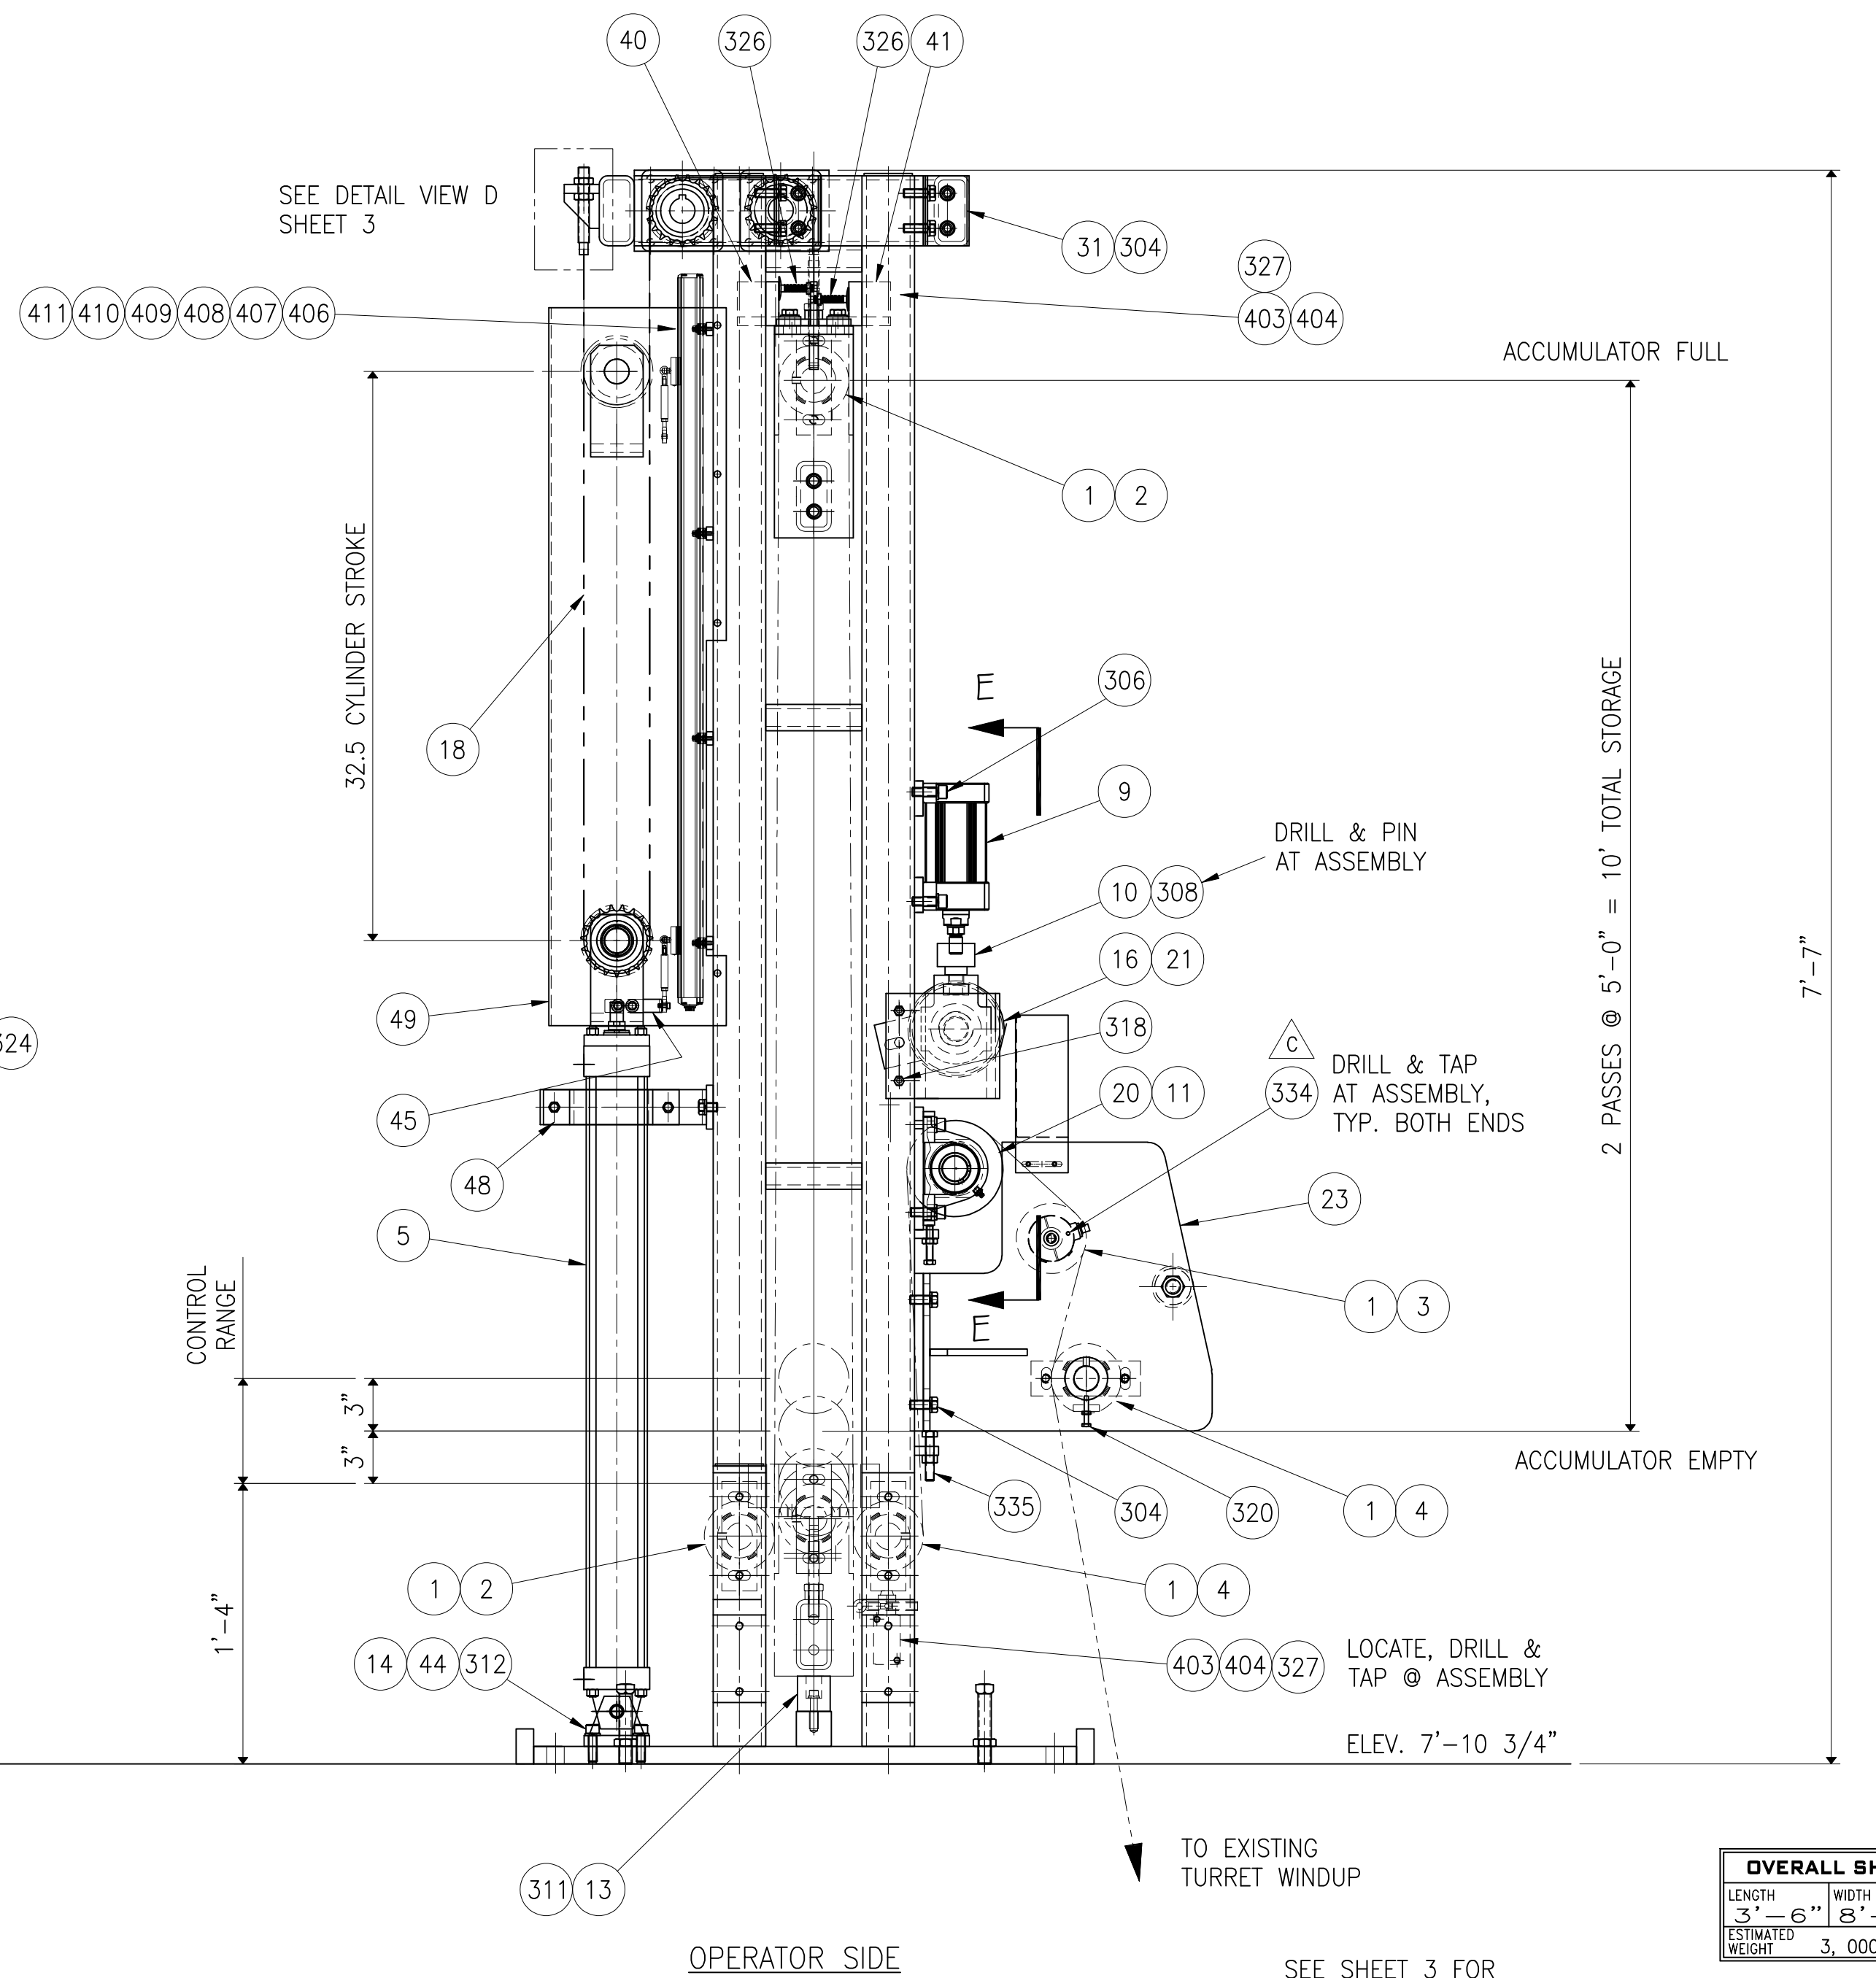

| OVERALL SHIPPING SIZE      |       |        |
|----------------------------|-------|--------|
| LENGTH                     | WIDTH | HEIGHT |
| 3'-6"                      | 8'-2" | 7'-8"  |
| ESTIMATED WEIGHT 3,000 LBS |       |        |

SEE SHEET 3 FOR  
SECTION VIEW DETAILS

FOR SECTIONS: 01.01 AND 02.01


REVISIONS

- ECO# 6485 JLC 1/19/26 SEE SHT.03  
ECO# 7053 JAY 4/23/26  
ADDED ITEMS: 55, 332-336  
CHANGE ITEM# 328 TO 332
- ECO# 7099 JLC 5/5/26  
ITEM 326 MADE NOT USED  
REPLACE BY ITEM 337



THIS DRAWING IS THE PROPERTY OF C. A. LITZLER CO., INC. AND IS LOANED SUBJECT TO RETURN UPON DEMAND. BORROWER AGREES THAT SAME WILL NOT BE USED IN ANY WAY DETRIMENTAL TO OWNER'S INTEREST.

C. A. LITZLER CO., INC. ASSUMES NO RESPONSIBILITY, EITHER DIRECT OR INDIRECT, FOR ANY CHANGES IN ENGINEERING DESIGN, COMPLETENESS OF DESIGN, SUBSTITUTION OF MATERIALS OR SUBSTITUTION OR ALTERATION OF COMMERCIAL SUPPLIED OR FABRICATED COMPONENTS NOT IN COMPLETE UNIFORMITY WITH ITS DRAWINGS AND INSTRUCTIONS, UNLESS SUCH DESIGN CHANGES, DELETIONS, SUBSTITUTIONS OR ALTERATIONS ARE FIRST APPROVED BY C. A. LITZLER CO., INC. IN WRITING.

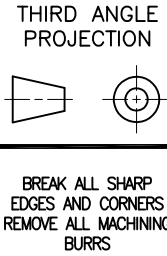


| UNLESS OTHERWISE SPECIFIED                                                           |                        |
|--------------------------------------------------------------------------------------|------------------------|
| ALL DIMENSIONS ARE EXPRESSED IN INCHES/MILLIMETERS                                   |                        |
| ALLOWABLE VARIATIONS:                                                                |                        |
| ENGLISH UNITS                                                                        | METRIC UNITS           |
| FRACTIONS: 1/16"                                                                     | NO. DECIMALS: ± 0.15mm |
| DECIMALS: .005"                                                                      | DECIMALS: .1mm         |
| ANGLES: 1/2°                                                                         | ANGLES: 1/2°           |
| ON METRIC ASSEMBLY DRAWINGS ROUND DECIMAL DIMENSIONS TO THE NEAREST WHOLE MILLIMETER |                        |

| DRAWING APPROVAL                        |      |
|-----------------------------------------|------|
| □ APPROVED AS DRAWN □ APPROVED AS NOTED |      |
| NAME                                    | DATE |

| C. A. LITZLER CO., INC.                                                                       |             |
|-----------------------------------------------------------------------------------------------|-------------|
| CLEVELAND, OHIO 44135-2689, U.S.A. 216-267-8020 (FAX) 216-267-8856 WEBSITE: WWW.CALITZLER.COM |             |
| TITLE                                                                                         | DWG. NO.    |
| WINDER ACCUMULATOR ASSEMBLY                                                                   | DA18117 01C |
| FOR                                                                                           | REV.        |
| DRAWN BY JAY 12/04/15                                                                         |             |
| CHECKED BY                                                                                    |             |
| APPROVED BY JLC                                                                               |             |
| APPROVED BY RFK                                                                               |             |

|                        |                |
|------------------------|----------------|
| JOB NUMBER: 2058       | SECTION: NOTED |
| SCALE: 1 1/2" = 1'-0"  |                |
| TOTAL DRAWING SHEETS 3 |                |

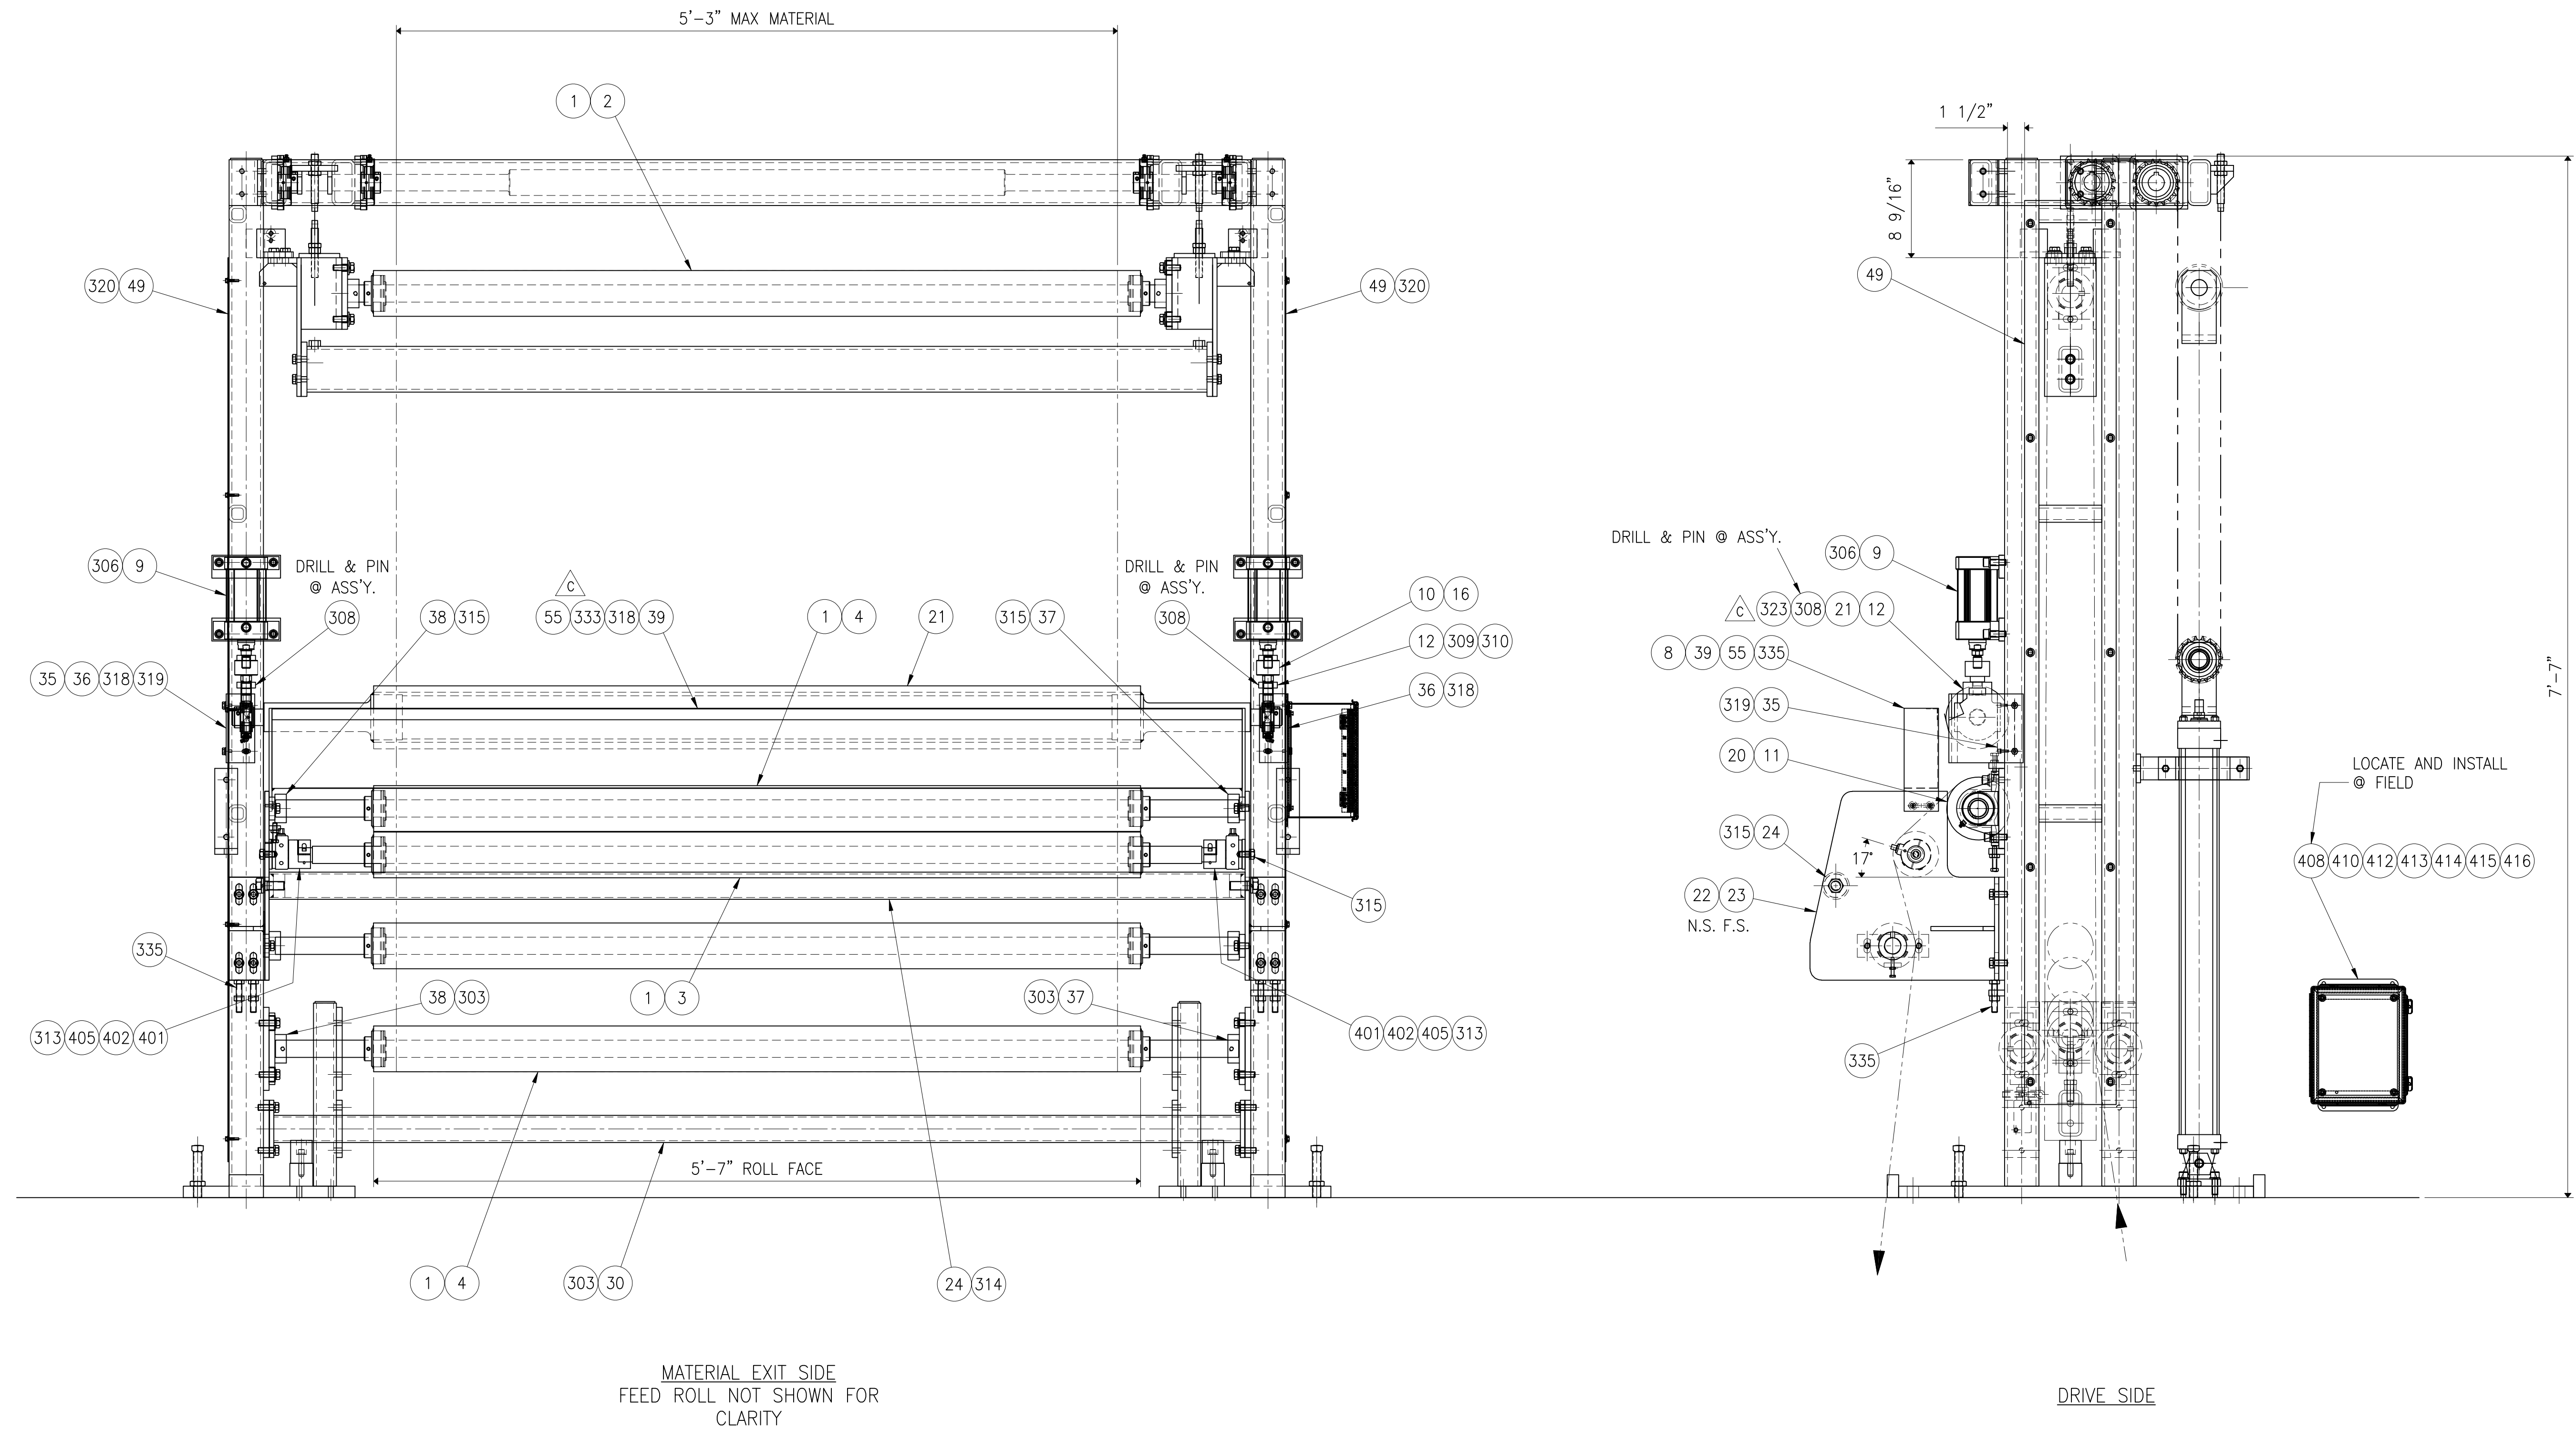


REVISIONS

ECO# 7053 JAY 4/23/26  
ADDED ITEMS: 55, 332-336  
CHANGE ITEM# 328 TO 332



THIS DRAWING IS THE PROPERTY OF C. A. LITZLER CO., INC. AND IS LOANED SUBJECT TO RETURN UPON DEMAND. BORROWER AGREES THAT SAME WILL NOT BE USED IN ANY WAY DETRIMENTAL TO OWNER'S INTEREST.

C. A. LITZLER CO., INC. ASSUMES NO RESPONSIBILITY, EITHER DIRECT OR INDIRECT, FOR ANY CHANGES IN ENGINEERING DESIGN, COMPLETENESS OF DESIGN, SUBSTITUTION OF MATERIALS OR FABRICATED COMPONENTS NOT IN COMPLETE UNIFORMITY WITH ITS DRAWINGS AND INSTRUCTIONS, UNLESS SUCH DESIGN CHANGES, DELETIONS, SUBSTITUTIONS OR ALTERATIONS ARE FIRST APPROVED BY C. A. LITZLER CO., INC. IN WRITING.

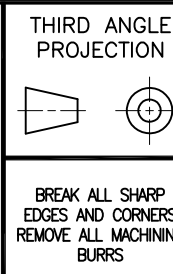

UNLESS OTHERWISE SPECIFIED  
ALL DIMENSIONS ARE EXPRESSED IN INCHES/MILLIMETERS

| ALLOWABLE VARIATIONS:       |                            |                   |
|-----------------------------|----------------------------|-------------------|
| ENGLISH UNITS               | METRIC UNITS               |                   |
| FRACTIONS: $\pm 1/16"$      | NO DECIMALS: $\pm 1.5mm$   |                   |
| DECIMALS: $.XX = \pm .005"$ | DECIMALS: $.X = \pm .05mm$ |                   |
|                             | $.XX = \pm .005"$          | $.XX = \pm .05mm$ |

ON METRIC ASSEMBLY DRAWINGS ROUND DECIMAL DIMENSIONS TO THE NEAREST WHOLE MILLIMETER

DRAWING APPROVAL

☐ APPROVED AS DRAWN ☐ APPROVED AS NOTED

NAME \_\_\_\_\_ DATE \_\_\_\_\_

**C. A. LITZLER CO., INC.**  
CLEVELAND, OHIO 44135-2688, U.S.A. 216-267-8020 (FAX) 216-267-9856 WEBSITE: WWW.CAUTLITZLER.COM

TITLE: WINDER ACCUMULATOR ASSEMBLY


FOR: \_\_\_\_\_

|             |     |          |
|-------------|-----|----------|
| DRAWN BY    | JAY | 12/04/15 |
| CHECKED BY  | JLC |          |
| APPROVED BY | JLC |          |
| APPROVED BY | RFK |          |




FOR SECTIONS: 01.01 AND 02.01

|                        |                |
|------------------------|----------------|
| JOB NUMBER: 2058       | SECTION: NOTED |
| SCALE: 1 1/2" = 1'-0"  |                |
| DWG. NO. DA18117       | 02 C           |
| TOTAL DRAWING SHEETS 3 |                |

REF. DWG. DA1520102A

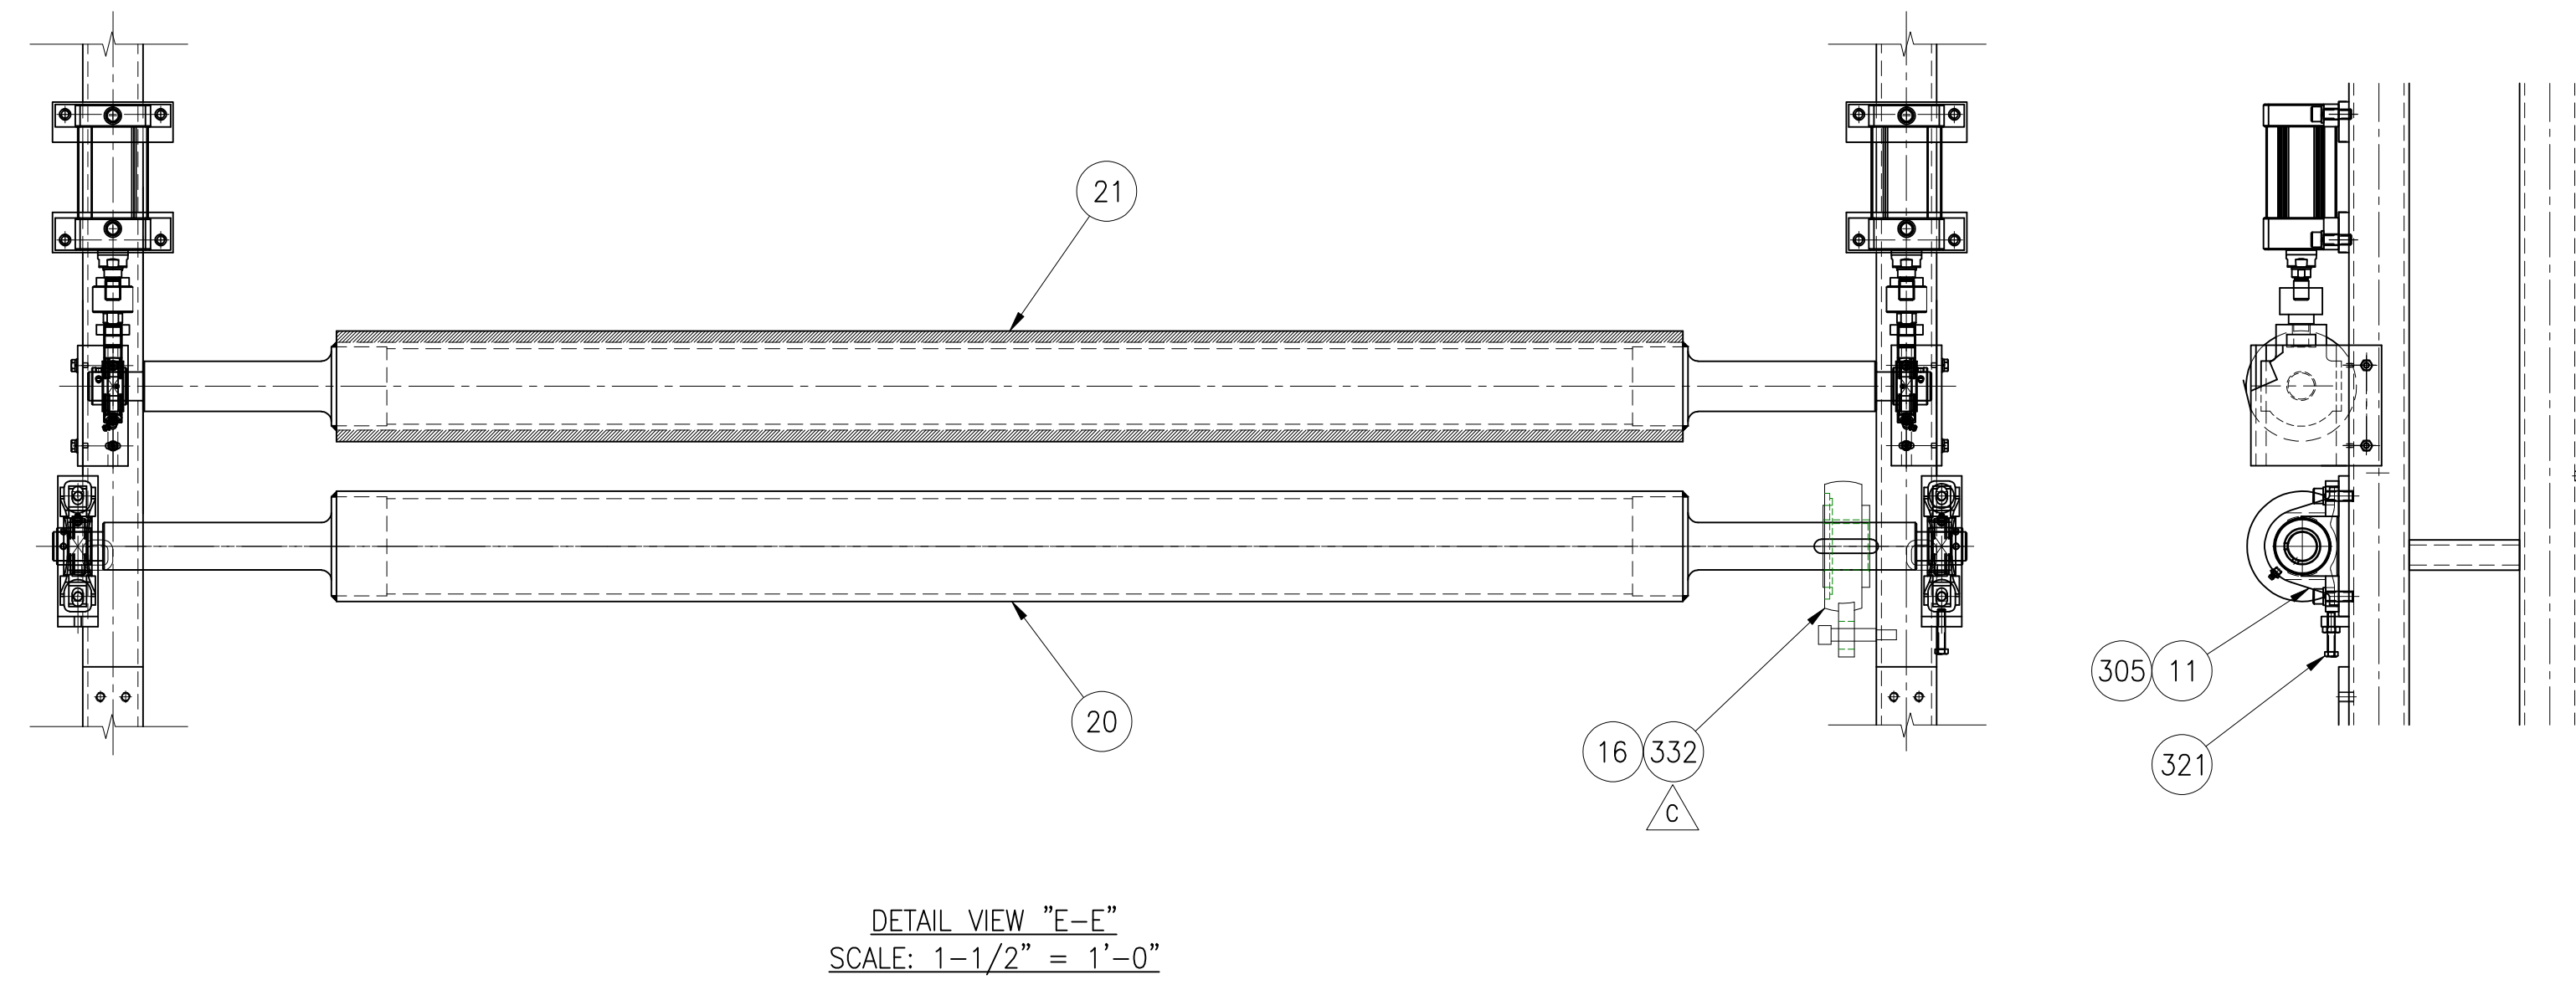

| OVERALL SHIPPING SIZE |                    |                  |
|-----------------------|--------------------|------------------|
| LENGTH<br>13'-7 3/4"  | WIDTH<br>6'-0 3/8" | HEIGHT<br>11'-3" |
| ESTIMATED WEIGHT      |                    | 2770 LBS         |

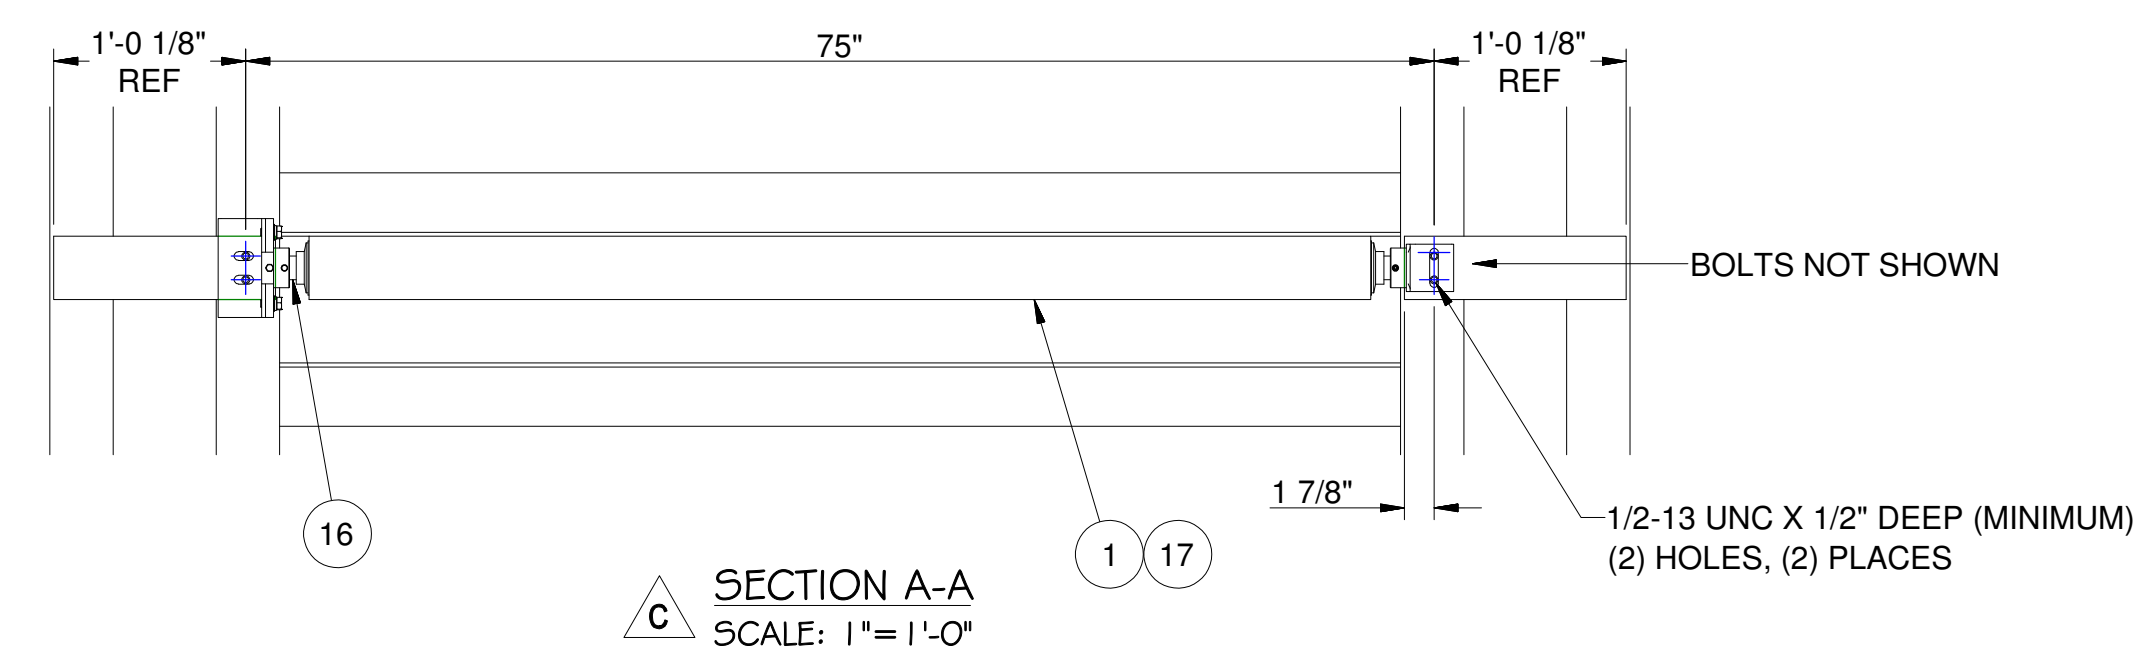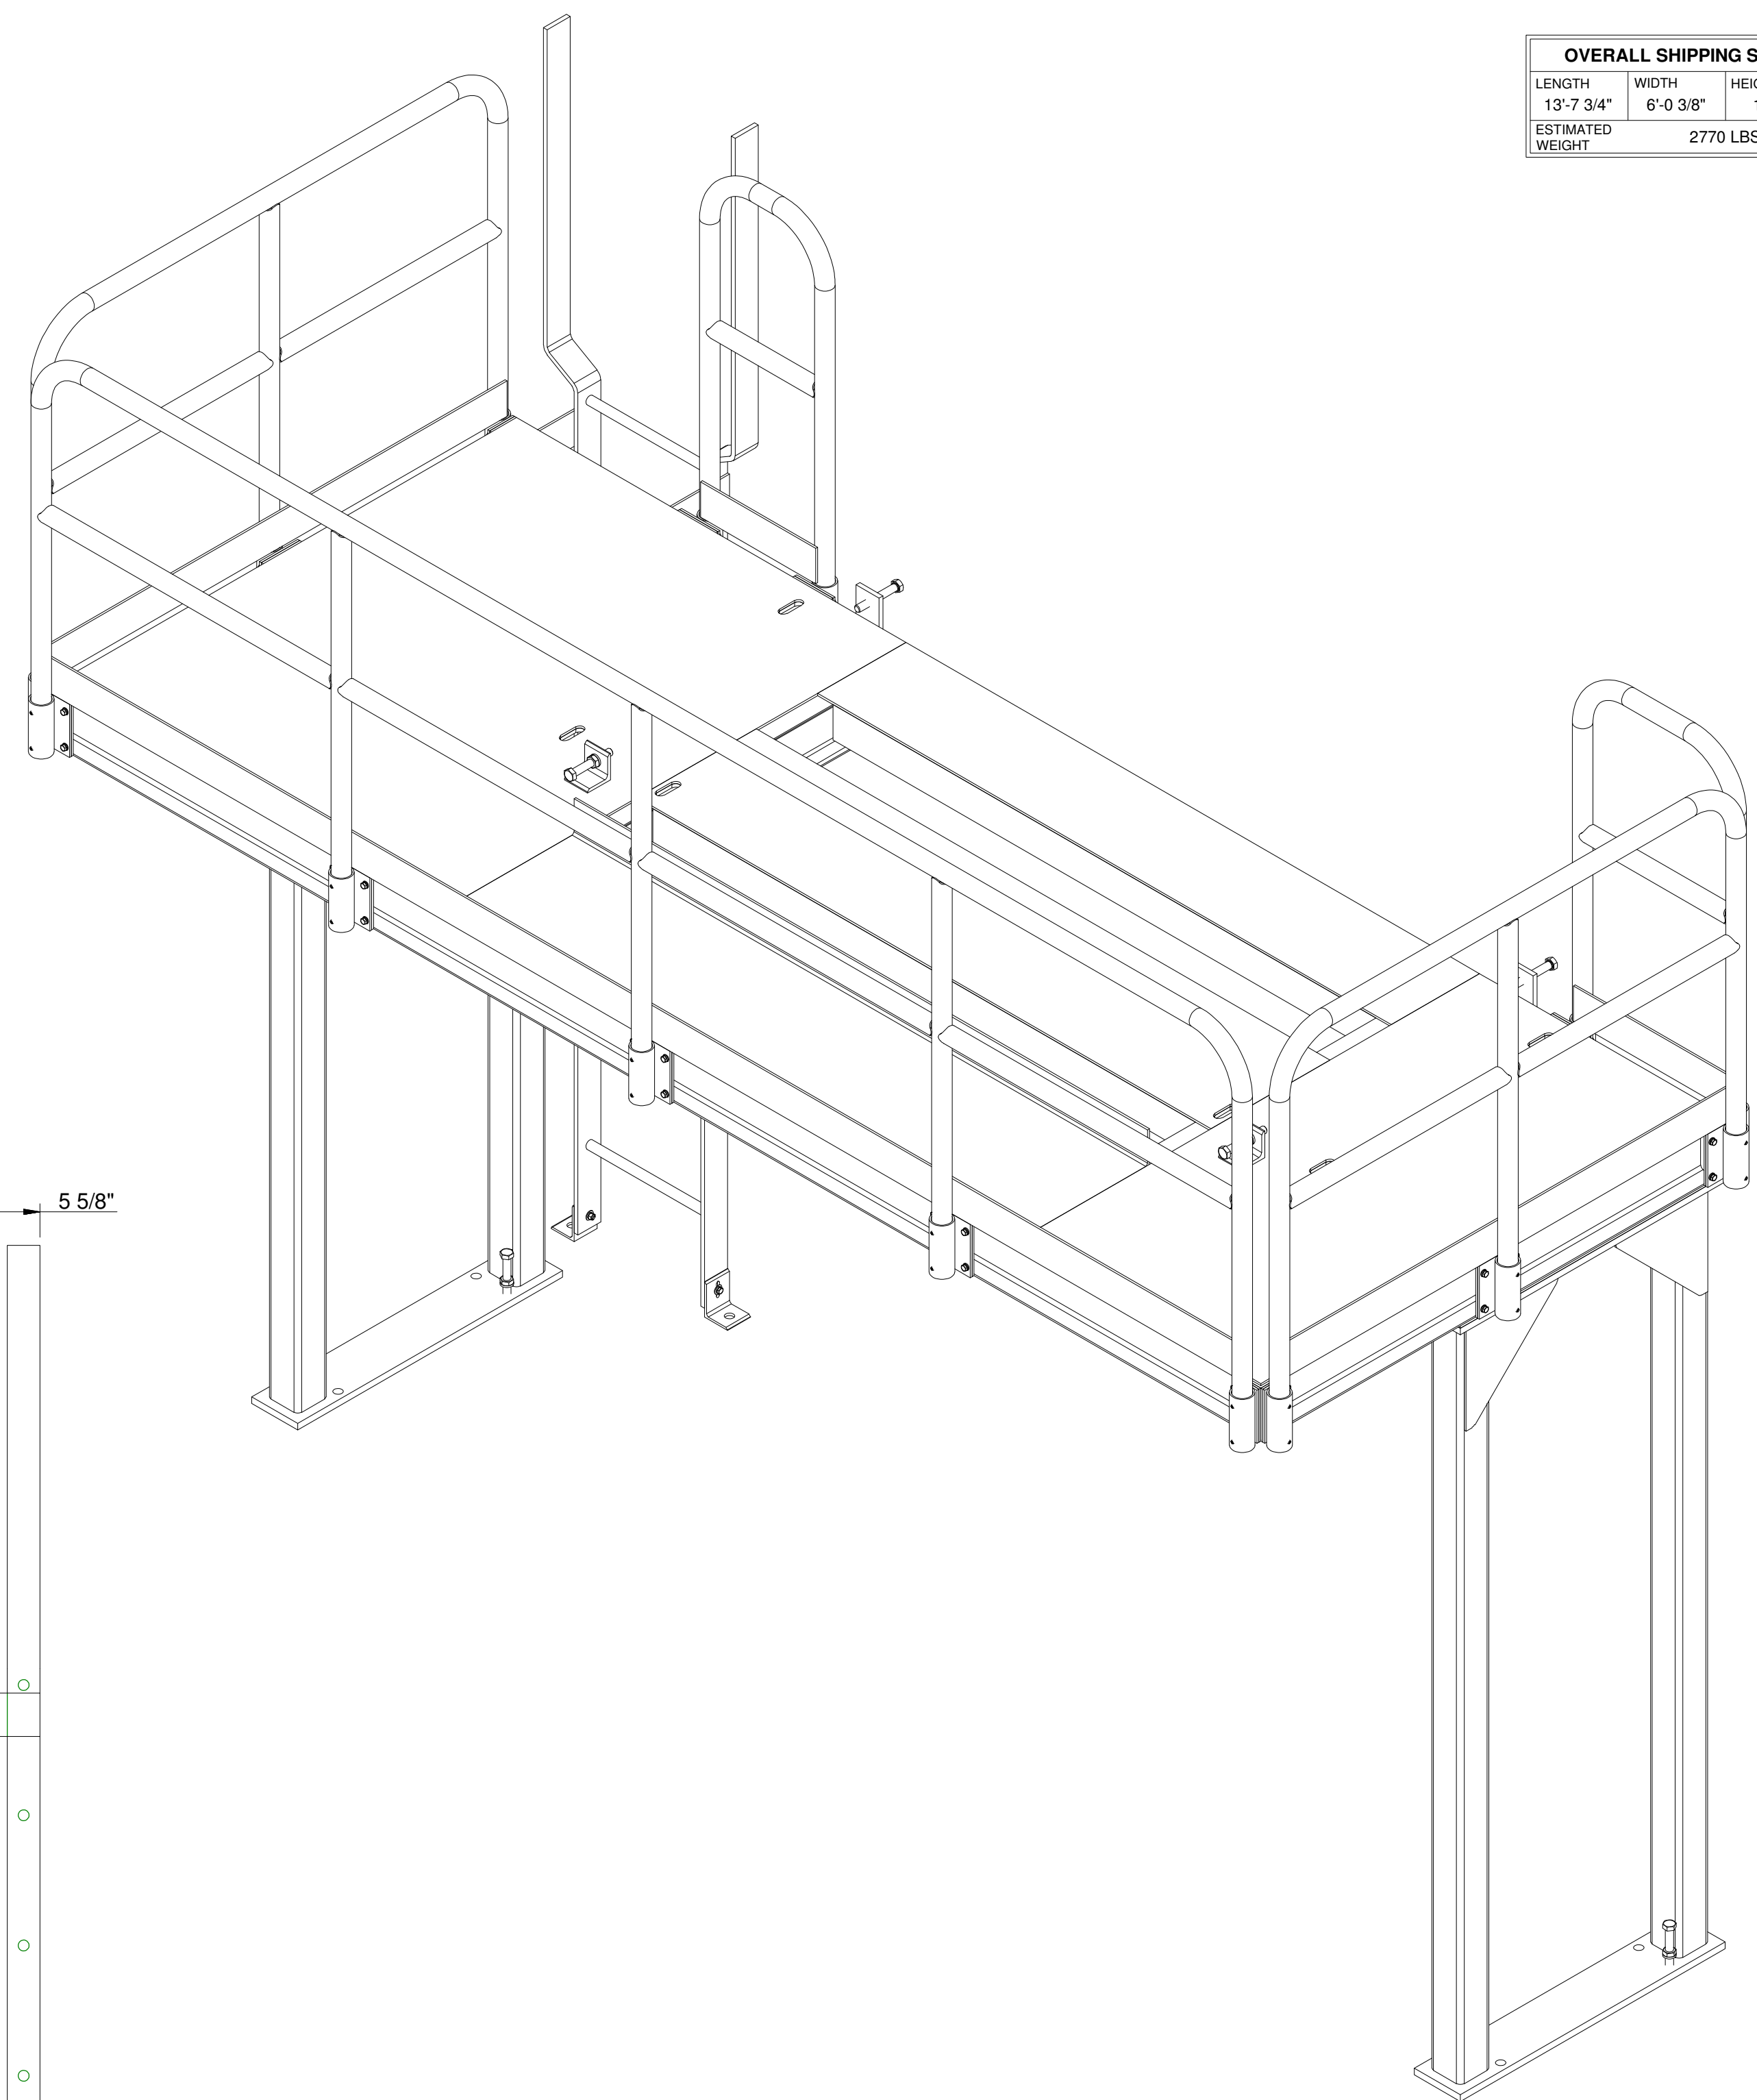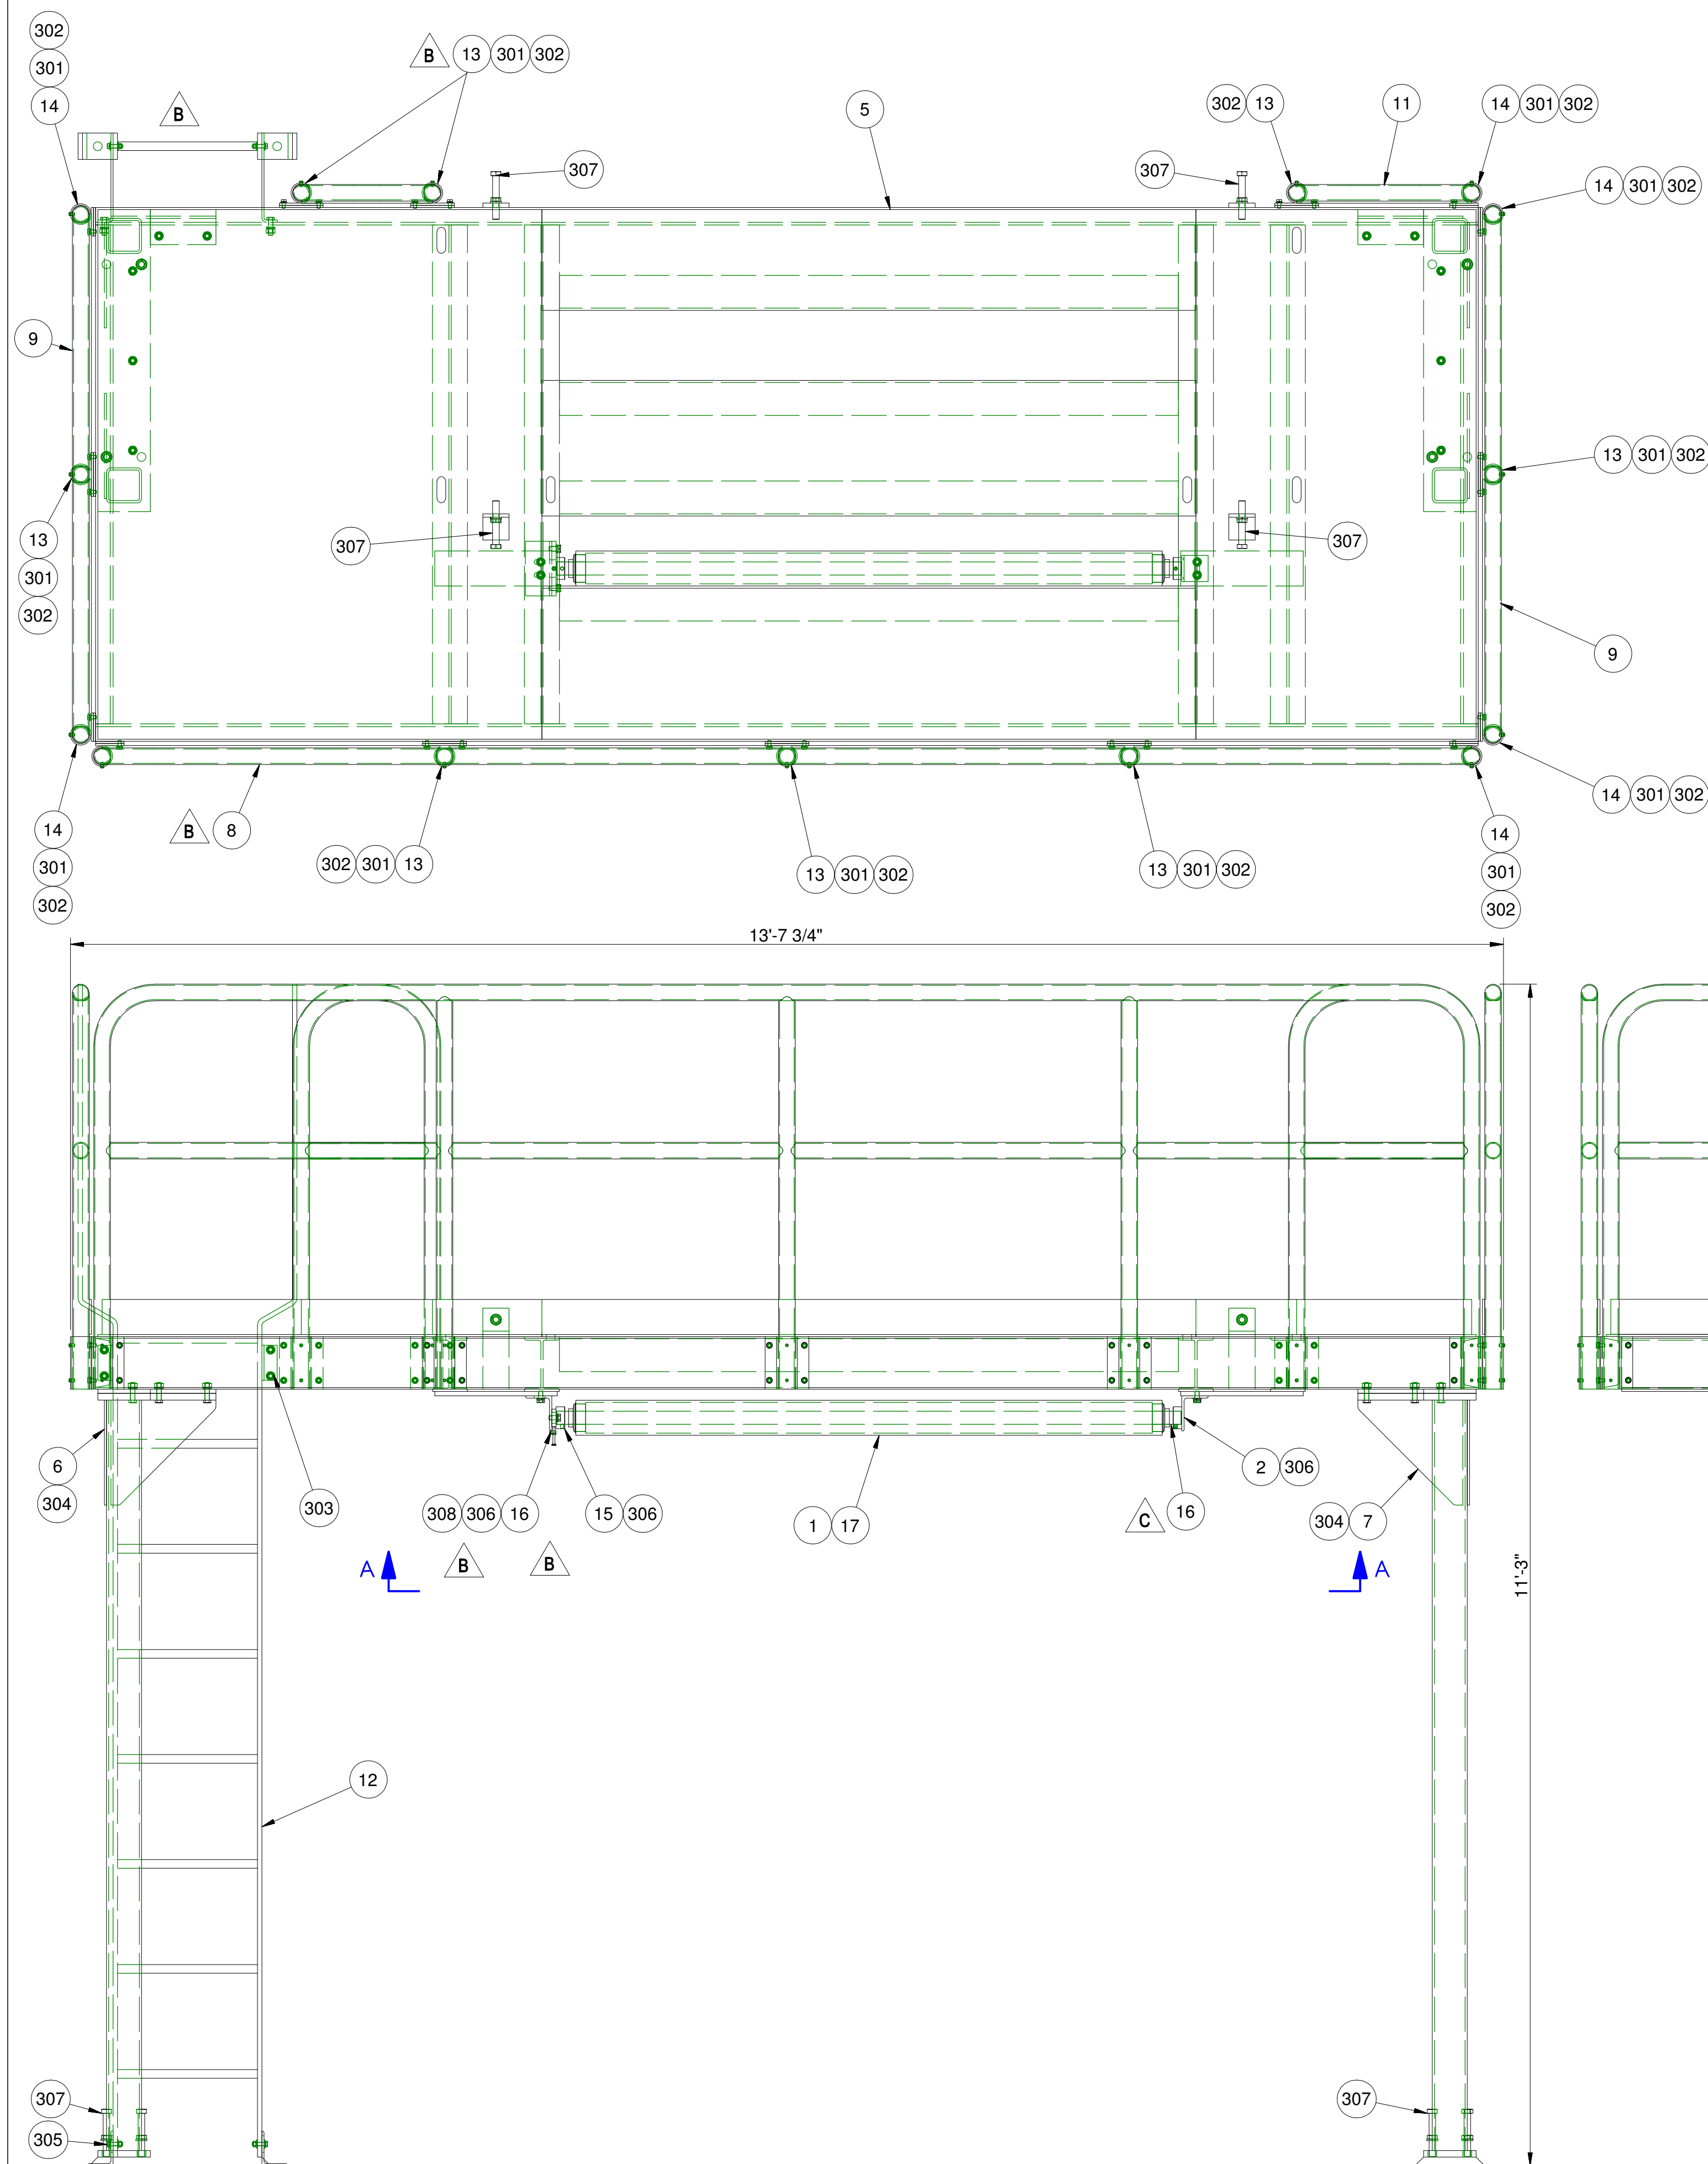

SECTIONS 01.02 & 02.02

REVISIONS

B

ECO 6482 DPB 1/15/26  
RELOCATE LADDER  
REV ITEMS 5, 8, 10  
ADDED ITEMS 15, 16, 308  
ITEM 306 QTY (6)

C

ECO #7059 RJB 4/24/26  
ADDED VIEW A-A; REPLACED  
ITEM #2 WITH #17

WAE CO.

Hot Metal Prepping  
by LITZLER

LITZLER

AUTOMATION  
DRIVES & CONTROLS

PSC

RADIO FREQUENCY by LITZLER

M&CT

MOLDING & COATING TECHNOLOGIES

Quickdraft®

Computerized Drafting Systems  
by LITZLER

THIS DRAWING IS THE PROPERTY OF C. A. LITZLER CO., INC. AND IS LOANED  
SUBJECT TO RETURN UPON DEMAND. RESPONSIBILITY EITHER THAT SAME WILL  
NOT BE USED IN ANY WAY DETRIMENTAL TO OWNERS INTEREST.

C. A. LITZLER CO., INC. ASSUMES NO RESPONSIBILITY EITHER DIRECT OR  
INDIRECT, FOR ANY CHANGES IN ENGINEERING DESIGN, COMPLETENESS OF  
DESIGN, OR SUBSTITUTION OF MATERIAL OR METHOD OF FABRICATION OF  
COMMERCIALY SUPPLIED OR FABRICATED COMPONENTS NOT IN COMPLETE  
UNIFORMITY WITH INSTRUCTIONS. UNLESS SUCH DESIGN CHANGES, DELETIONS,  
SUBSTITUTIONS OR ALTERATIONS ARE FIRST APPROVED BY  
C. A. LITZLER CO., INC. IN WRITING.

UNLESS OTHERWISE SPECIFIED

| ALL DUAL DIMENSIONS ARE<br>EXPRESSED IN INCHES/MILLIMETERS |                      |
|------------------------------------------------------------|----------------------|
| ALLOWABLE VARIATIONS                                       |                      |
| ENGLISH UNITS                                              | METRIC UNITS         |
| FRACTIONS: 1/16"                                           | NO DECIMALS: 1.5mm   |
| DECIMALS: .001" ± .001"                                    | DECIMALS: .1 ± .10mm |
|                                                            | .002" ± .002"        |
|                                                            | .005" ± .010mm       |
| ANGLES: 10° - 30°                                          |                      |

ON METRIC ASSEMBLY DRAWINGS ROUND  
DECIMAL DIMENSIONS TO THE NEAREST  
WHOLE MILLIMETER

THIRD ANGLE  
PROJECTION



BREAK ALL SHARP  
EDGES AND CORNERS  
REMOVE ALL MACHINING  
BURRS

DRAWING APPROVAL

☒ APPROVED AS DRAWN

☐ APPROVED AS NOTED

| NAME | DATE |
|------|------|
|      |      |

C. A. LITZLER CO., INC.

CLEVELAND, OHIO 44135-0888, U.S.A. 216-267-8020 (FAX) 216-267-8656

WEBSITE: WWW.CALITZLER.COM

| ACCUMULATOR PLATFORM |              |
|----------------------|--------------|
| TITLE                | DRAWN BY     |
|                      | DPB 12/18/25 |
| FOR                  | CHECKED BY   |
|                      | JLC 12/22/25 |
|                      | APPROVED BY  |
|                      | RFK 12/22/25 |

JOB NUMBER: 2058

SECTION: NOTED

SCALE: 1" = 1'-0"

DA18118

01

C


DWG. NO.

SH.

REV.

TOTAL DRAWING SHEETS 1

REF. DWG.

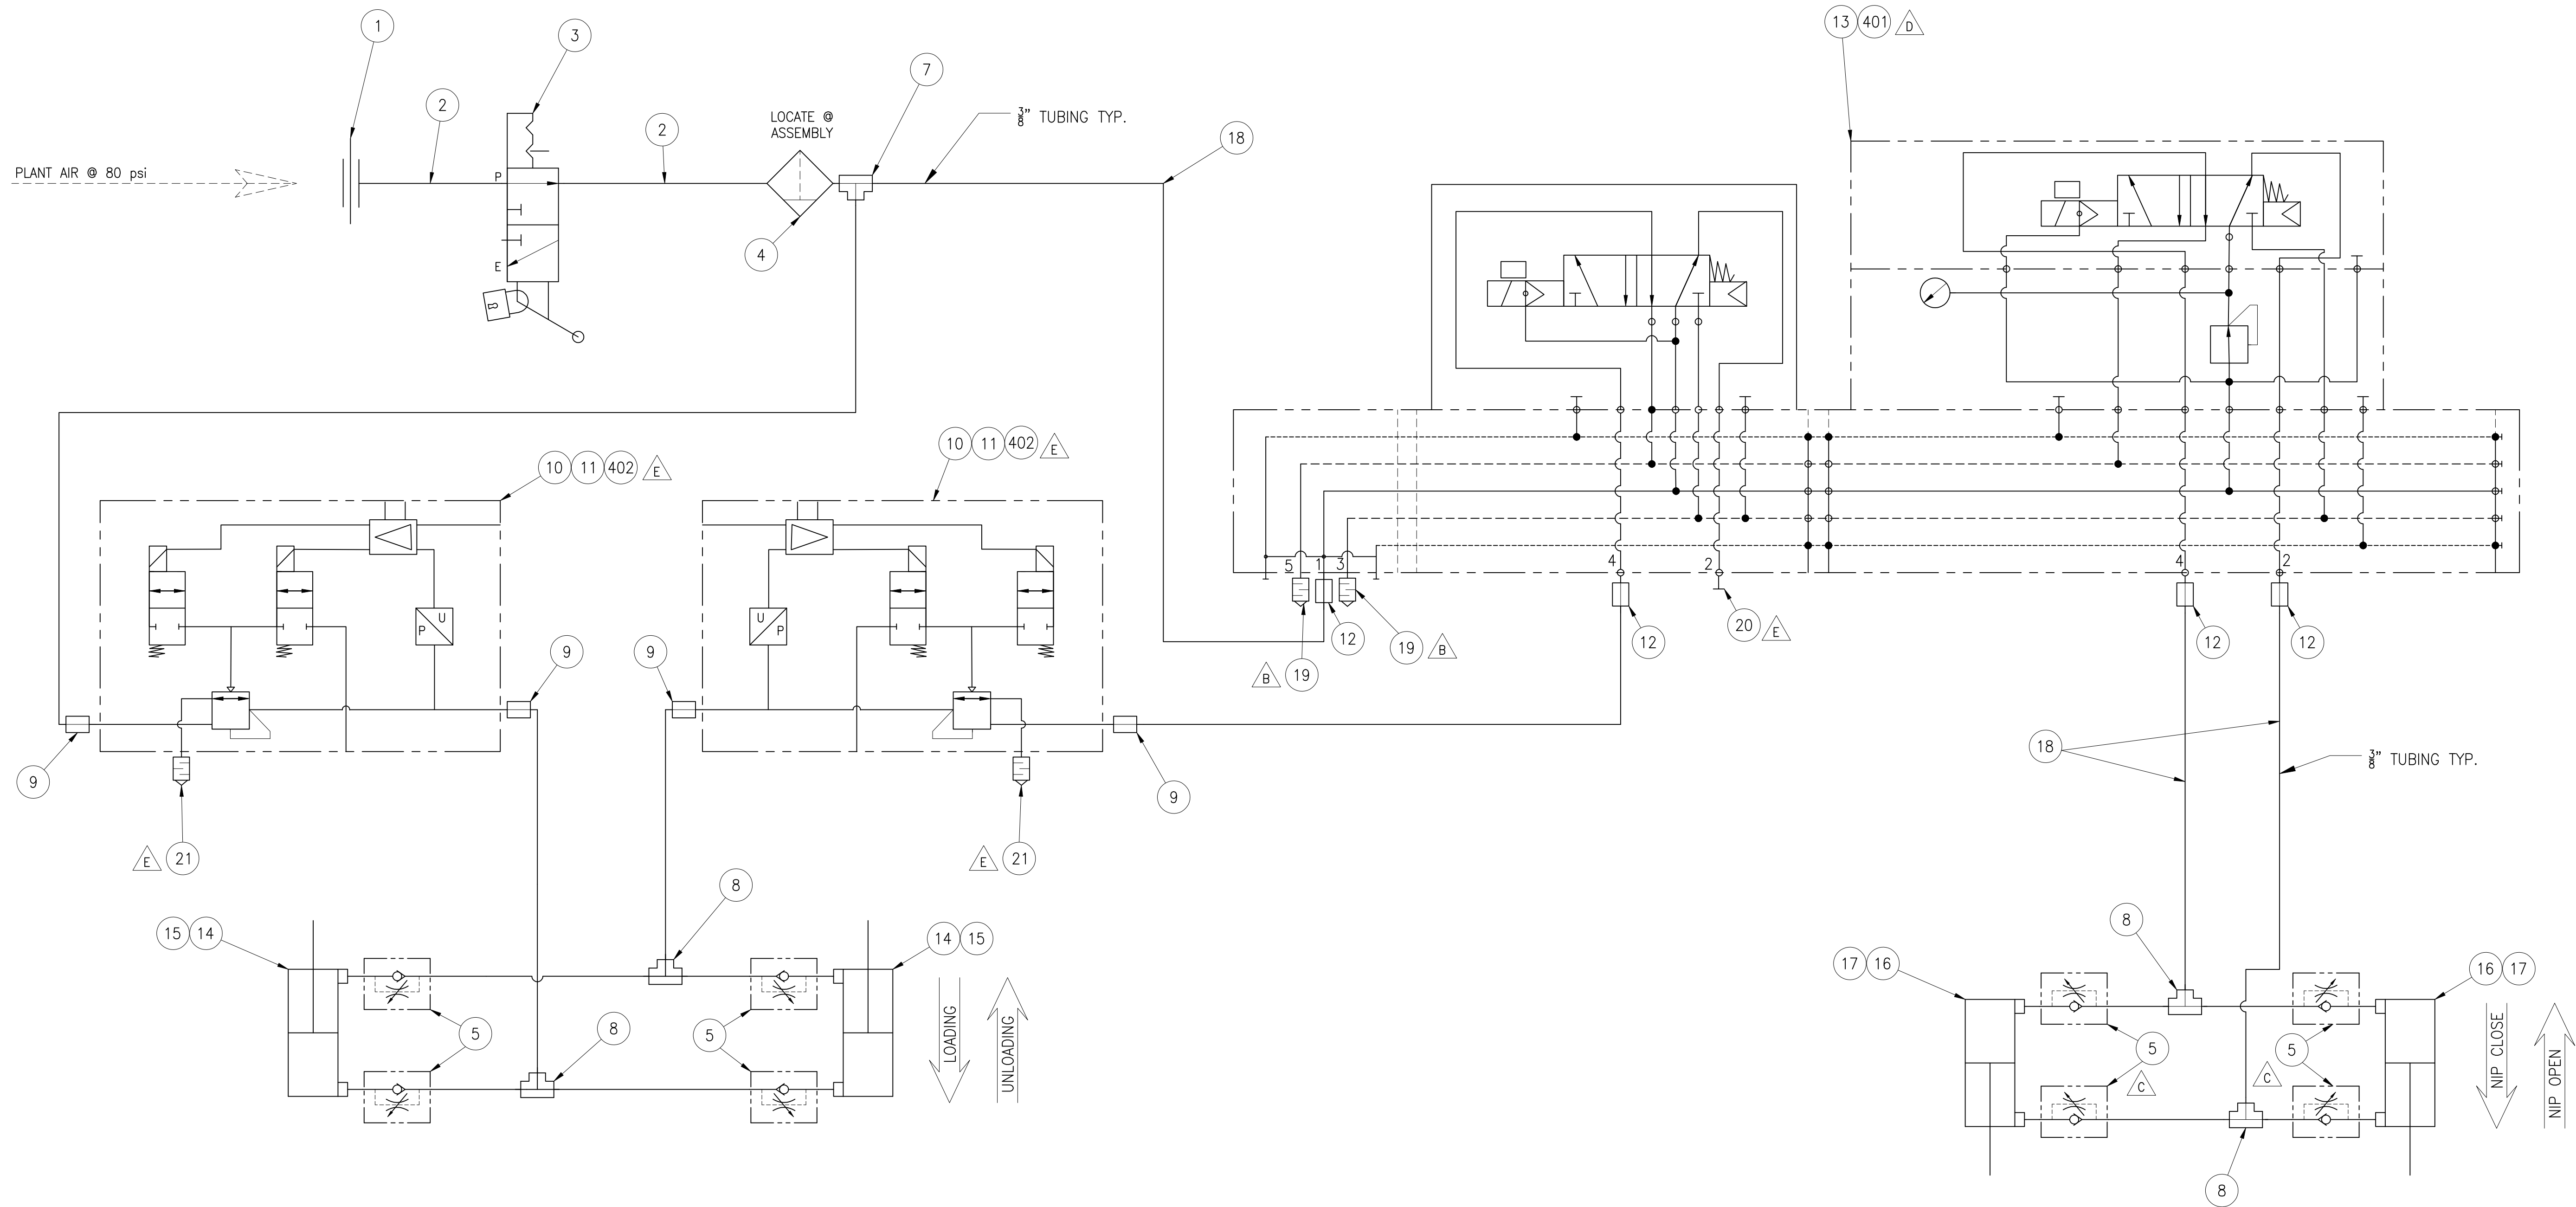


REVISIONS

|   |                                        |   |                                                   |
|---|----------------------------------------|---|---------------------------------------------------|
| B | ECO# 7067 JLC 4/28/26<br>ADDED ITEM 19 | E | ECO# 7098 JLC 5/04/26<br>ADDED ITEM 20, 21, & 402 |
| C | ECO# 7081 4/30/26<br>WAS ITEM 6        |   |                                                   |
| D | ECO# 7092 RFK 5/04/26<br>WAS ITEM 401  |   |                                                   |



THIS DRAWING IS THE PROPERTY OF C. A. LITZLER CO., INC. AND IS LOANED SUBJECT TO RETURN UPON DEMAND. BORROWER AGREES THAT SAME WILL NOT BE USED IN ANY WAY DETRIMENTAL TO OWNER'S INTEREST.

C. A. LITZLER CO., INC. ASSUMES NO RESPONSIBILITY, EITHER DIRECT OR INDIRECT, FOR ANY CHANGES IN ENGINEERING DESIGN, COMPLETENESS OF DESIGN, SUBSTITUTION OF MATERIALS OR SUBSTITUTION OR ALTERATION OF COMMERCIALLY SUPPLIED OR FABRICATED COMPONENTS NOT IN COMPLETE UNIFORMITY WITH ITS DRAWINGS AND INSTRUCTIONS, UNLESS SUCH DESIGN CHANGES, DELETIONS, SUBSTITUTIONS OR ALTERATIONS ARE FIRST APPROVED BY C. A. LITZLER CO., INC. IN WRITING.

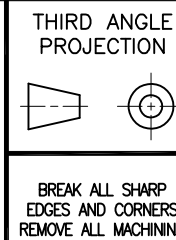

| UNLESS OTHERWISE SPECIFIED                                                           |                     |
|--------------------------------------------------------------------------------------|---------------------|
| ALL DIMENSIONS ARE EXPRESSED IN INCHES/MILLIMETERS                                   |                     |
| ALLOWABLE VARIATIONS:                                                                |                     |
| ENGLISH UNITS                                                                        | METRIC UNITS        |
| FRACTIONS: 1/16"                                                                     | NO DECIMALS: ±1.5mm |
| DECIMALS: .001" ±.002"                                                               | DECIMALS: .X ±.05mm |
| .001 ±.002                                                                           | .X ±.05mm           |
| ANGLES: 15°-30°                                                                      |                     |
| ON METRIC ASSEMBLY DRAWINGS ROUND DECIMAL DIMENSIONS TO THE NEAREST WHOLE MILLIMETER |                     |


| DRAWING APPROVAL                           |                                            |
|--------------------------------------------|--------------------------------------------|
| <input type="checkbox"/> APPROVED AS DRAWN | <input type="checkbox"/> APPROVED AS NOTED |
| NAME                                       | DATE                                       |

| C. A. LITZLER CO., INC.                                                                       |            |          |  |
|-----------------------------------------------------------------------------------------------|------------|----------|--|
| CLEVELAND, OHIO 44135-2689, U.S.A. 216-267-8020 (FAX) 216-267-9856 WEBSITE: WWW.CALITZLER.COM |            |          |  |
| TITLE                                                                                         | AIR PIPING |          |  |
| FOR                                                                                           |            |          |  |
| DRAWN BY                                                                                      | JLC        | 11/27/26 |  |
| CHECKED BY                                                                                    |            |          |  |
| APPROVED BY                                                                                   |            |          |  |
| APPROVED BY                                                                                   |            |          |  |

|                      |                    |
|----------------------|--------------------|
| JOB NUMBER: 2058     | SECTION: 1.03/2.03 |
| SCALE: NONE          |                    |
| DWG. NO.             | DA18119 01 E       |
| TOTAL DRAWING SHEETS | 1                  |


REF. DWG.

REVISIONS

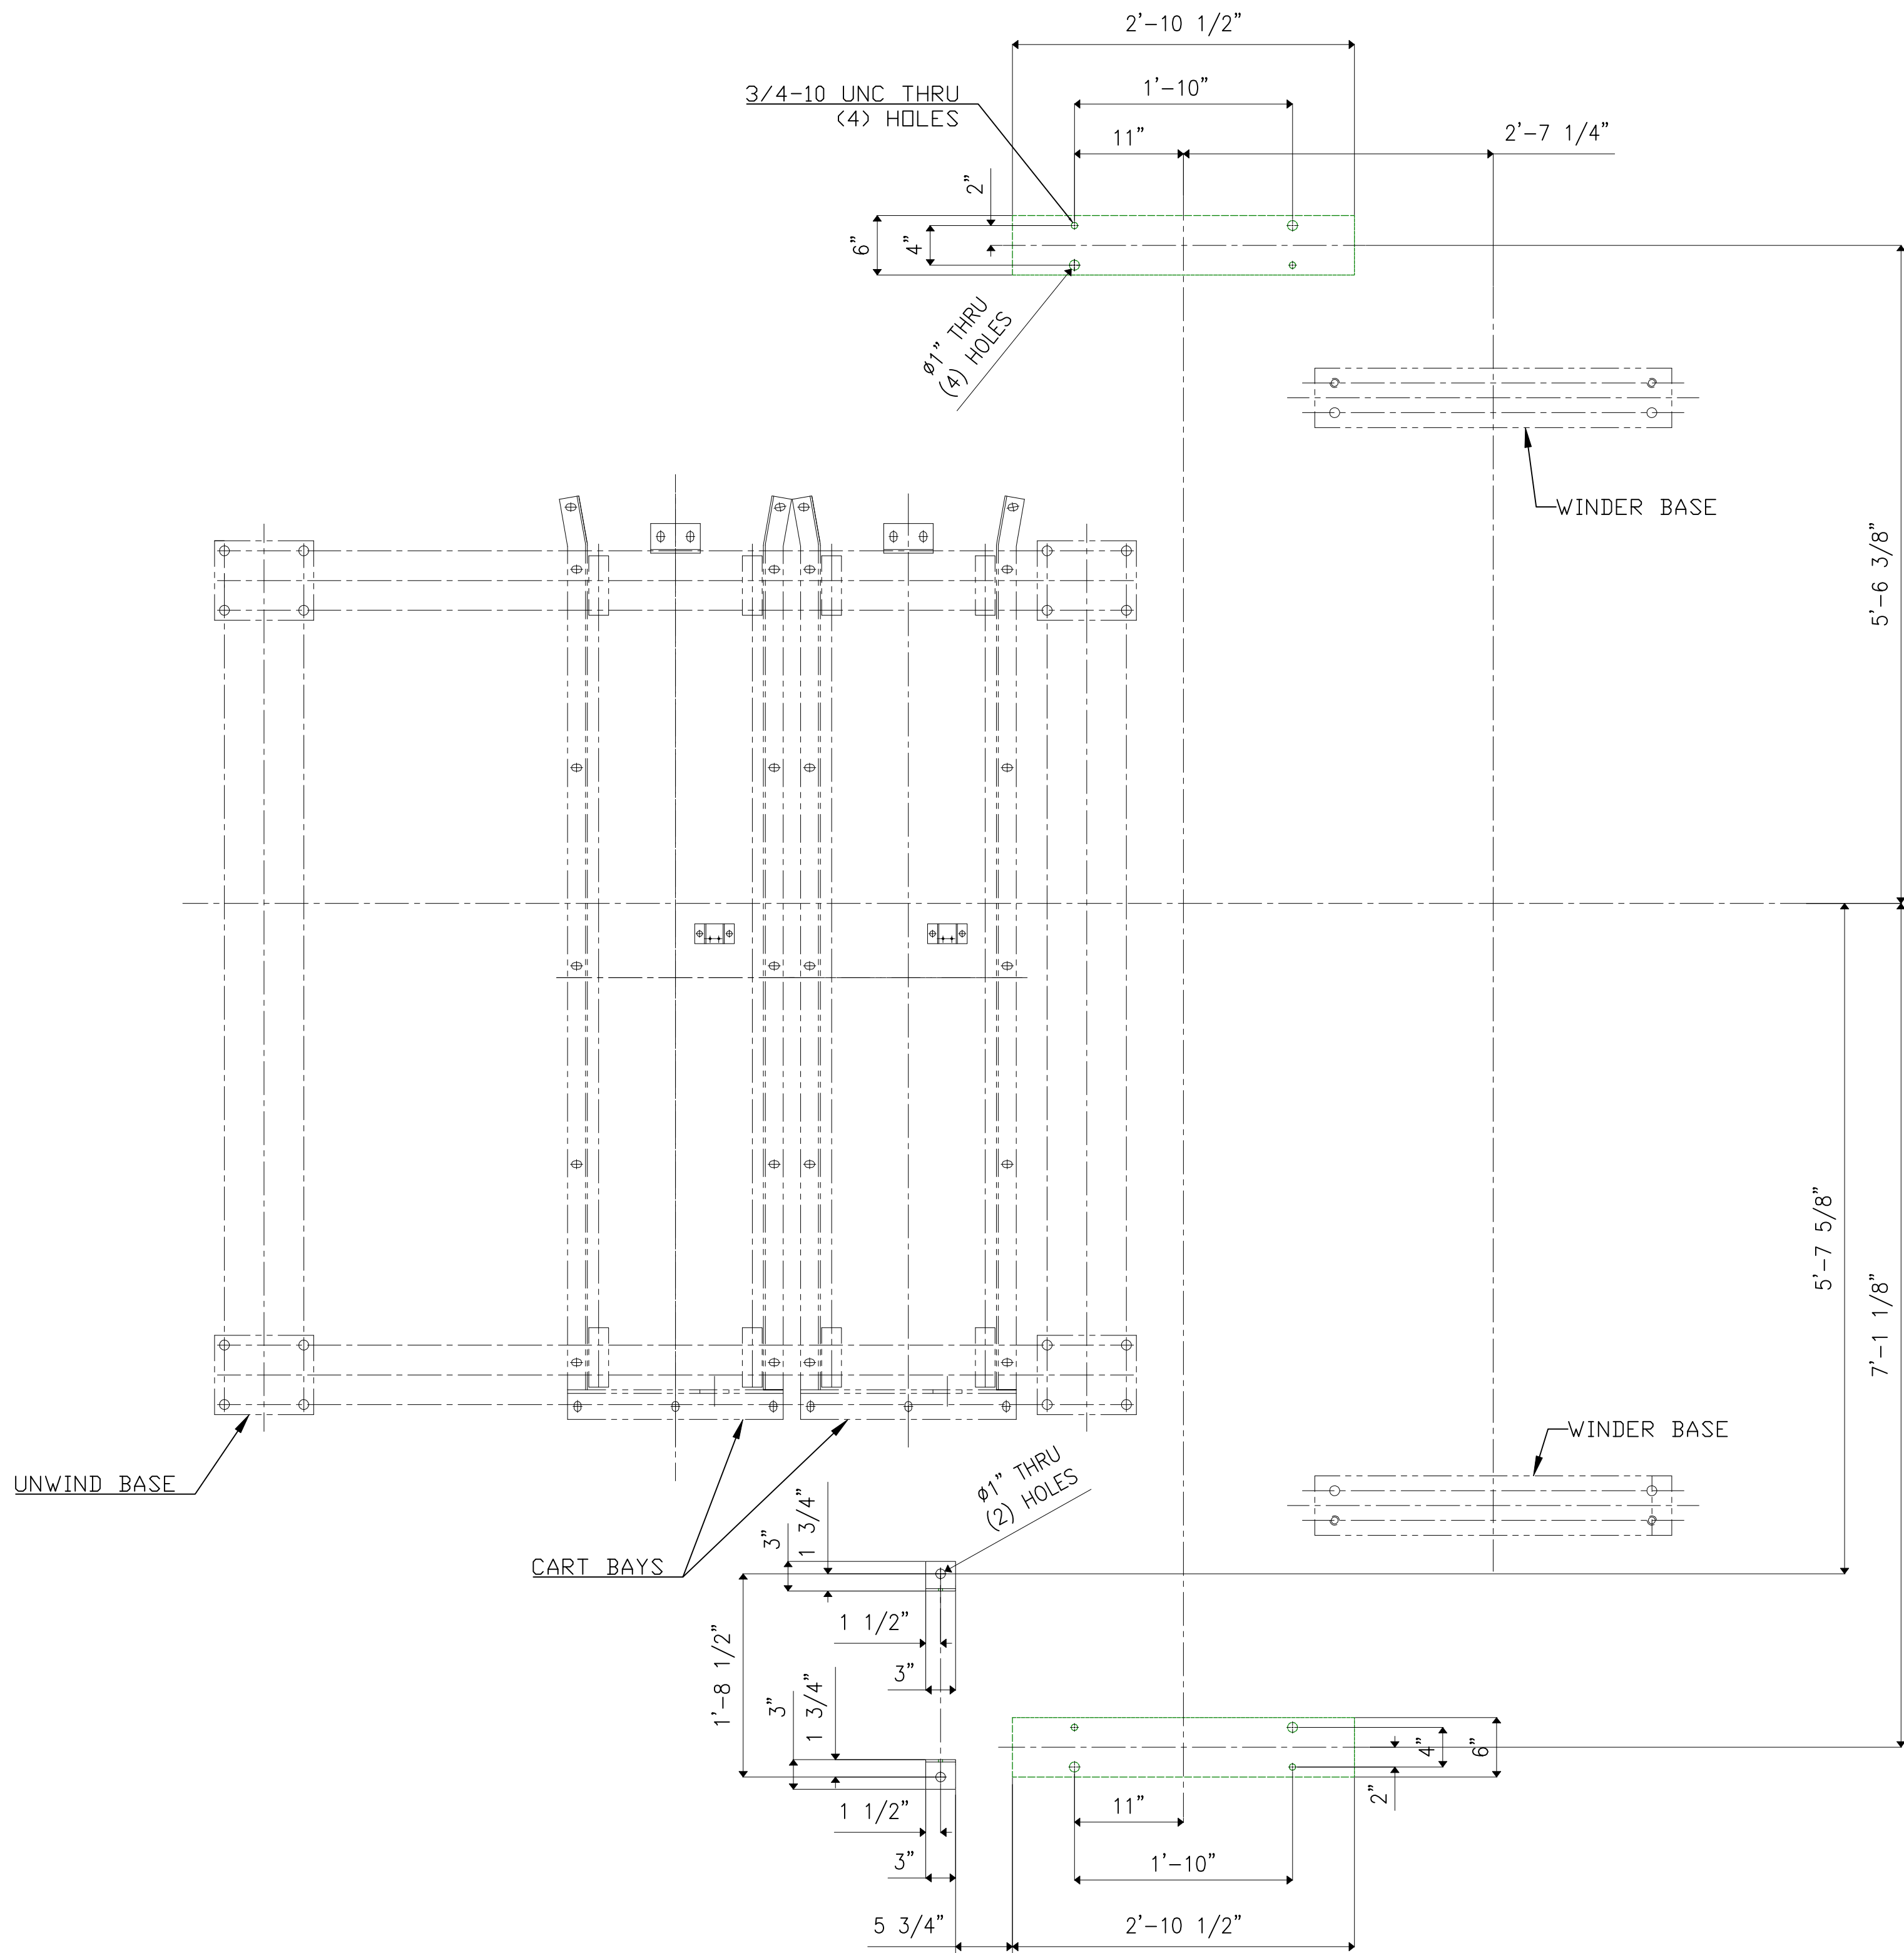

THIS DRAWING IS THE PROPERTY OF C. A. LITZLER CO., INC. AND IS LOANED SUBJECT TO RETURN UPON DEMAND. BORROWER AGREES THAT SAME WILL NOT BE USED IN ANY WAY DETRIMENTAL TO OWNER'S INTEREST.

C. A. LITZLER CO., INC. ASSUMES NO RESPONSIBILITY, EITHER DIRECT OR INDIRECT, FOR ANY CHANGES IN ENGINEERING DESIGN, COMPLETENESS OF DESIGN, SUBSTITUTION OF MATERIALS OR SUBSTITUTION OR ALTERATION OF COMMERCIALLY SUPPLIED OR FABRICATED COMPONENTS NOT IN COMPLETE UNIFORMITY WITH ITS DRAWINGS AND INSTRUCTIONS, UNLESS SUCH DESIGN CHANGES, DELETIONS, SUBSTITUTIONS OR ALTERATIONS ARE FIRST APPROVED BY C. A. LITZLER CO., INC. IN WRITING.

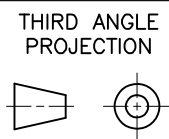

BREAK ALL SHARP EDGES AND CORNERS REMOVE ALL MACHINING BURRS

| UNLESS OTHERWISE SPECIFIED                                                           |                     |
|--------------------------------------------------------------------------------------|---------------------|
| ALL DIMENSIONS ARE EXPRESSED IN INCHES/MILLIMETERS                                   |                     |
| ALLOWABLE VARIATIONS:                                                                |                     |
| ENGLISH UNITS                                                                        | METRIC UNITS        |
| FRACTIONS: 1/16"                                                                     | NO DECIMALS ±1.5mm  |
| DECIMALS: .001 ±.002"                                                                | DECIMALS: X ±.005mm |
| ANGLES: 15°-30°                                                                      | Y ±.01mm            |
| ON METRIC ASSEMBLY DRAWINGS ROUND DECIMAL DIMENSIONS TO THE NEAREST WHOLE MILLIMETER |                     |


| DRAWING APPROVAL                           |                                            |
|--------------------------------------------|--------------------------------------------|
| <input type="checkbox"/> APPROVED AS DRAWN | <input type="checkbox"/> APPROVED AS NOTED |
| NAME                                       | DATE                                       |

| C. A. LITZLER CO., INC.                                                                       |                                    |             |              |
|-----------------------------------------------------------------------------------------------|------------------------------------|-------------|--------------|
| CLEVELAND, OHIO 44135-2689, U.S.A. 216-267-8020 (FAX) 216-267-9856 WEBSITE: WWW.CALITZLER.COM |                                    |             |              |
| TITLE                                                                                         | ACCUMULATOR PLATFORM AJ FOUNDATION | DRAWN BY    | DPB 12/18/25 |
| CHECKED BY                                                                                    | JLC 12/22/25                       | APPROVED BY | RFK 12/22/25 |
| FOR                                                                                           |                                    | APPROVED BY | RFK 12/22/25 |


|                        |                      |
|------------------------|----------------------|
| JOB NUMBER: 2058       | SECTION: 98.11       |
| SCALE: 1"=1'-0"        | DWG. NO. DA18123 01B |
| TOTAL DRAWING SHEETS 2 | SHT. REV.            |

REF. DWG.


REVISIONS

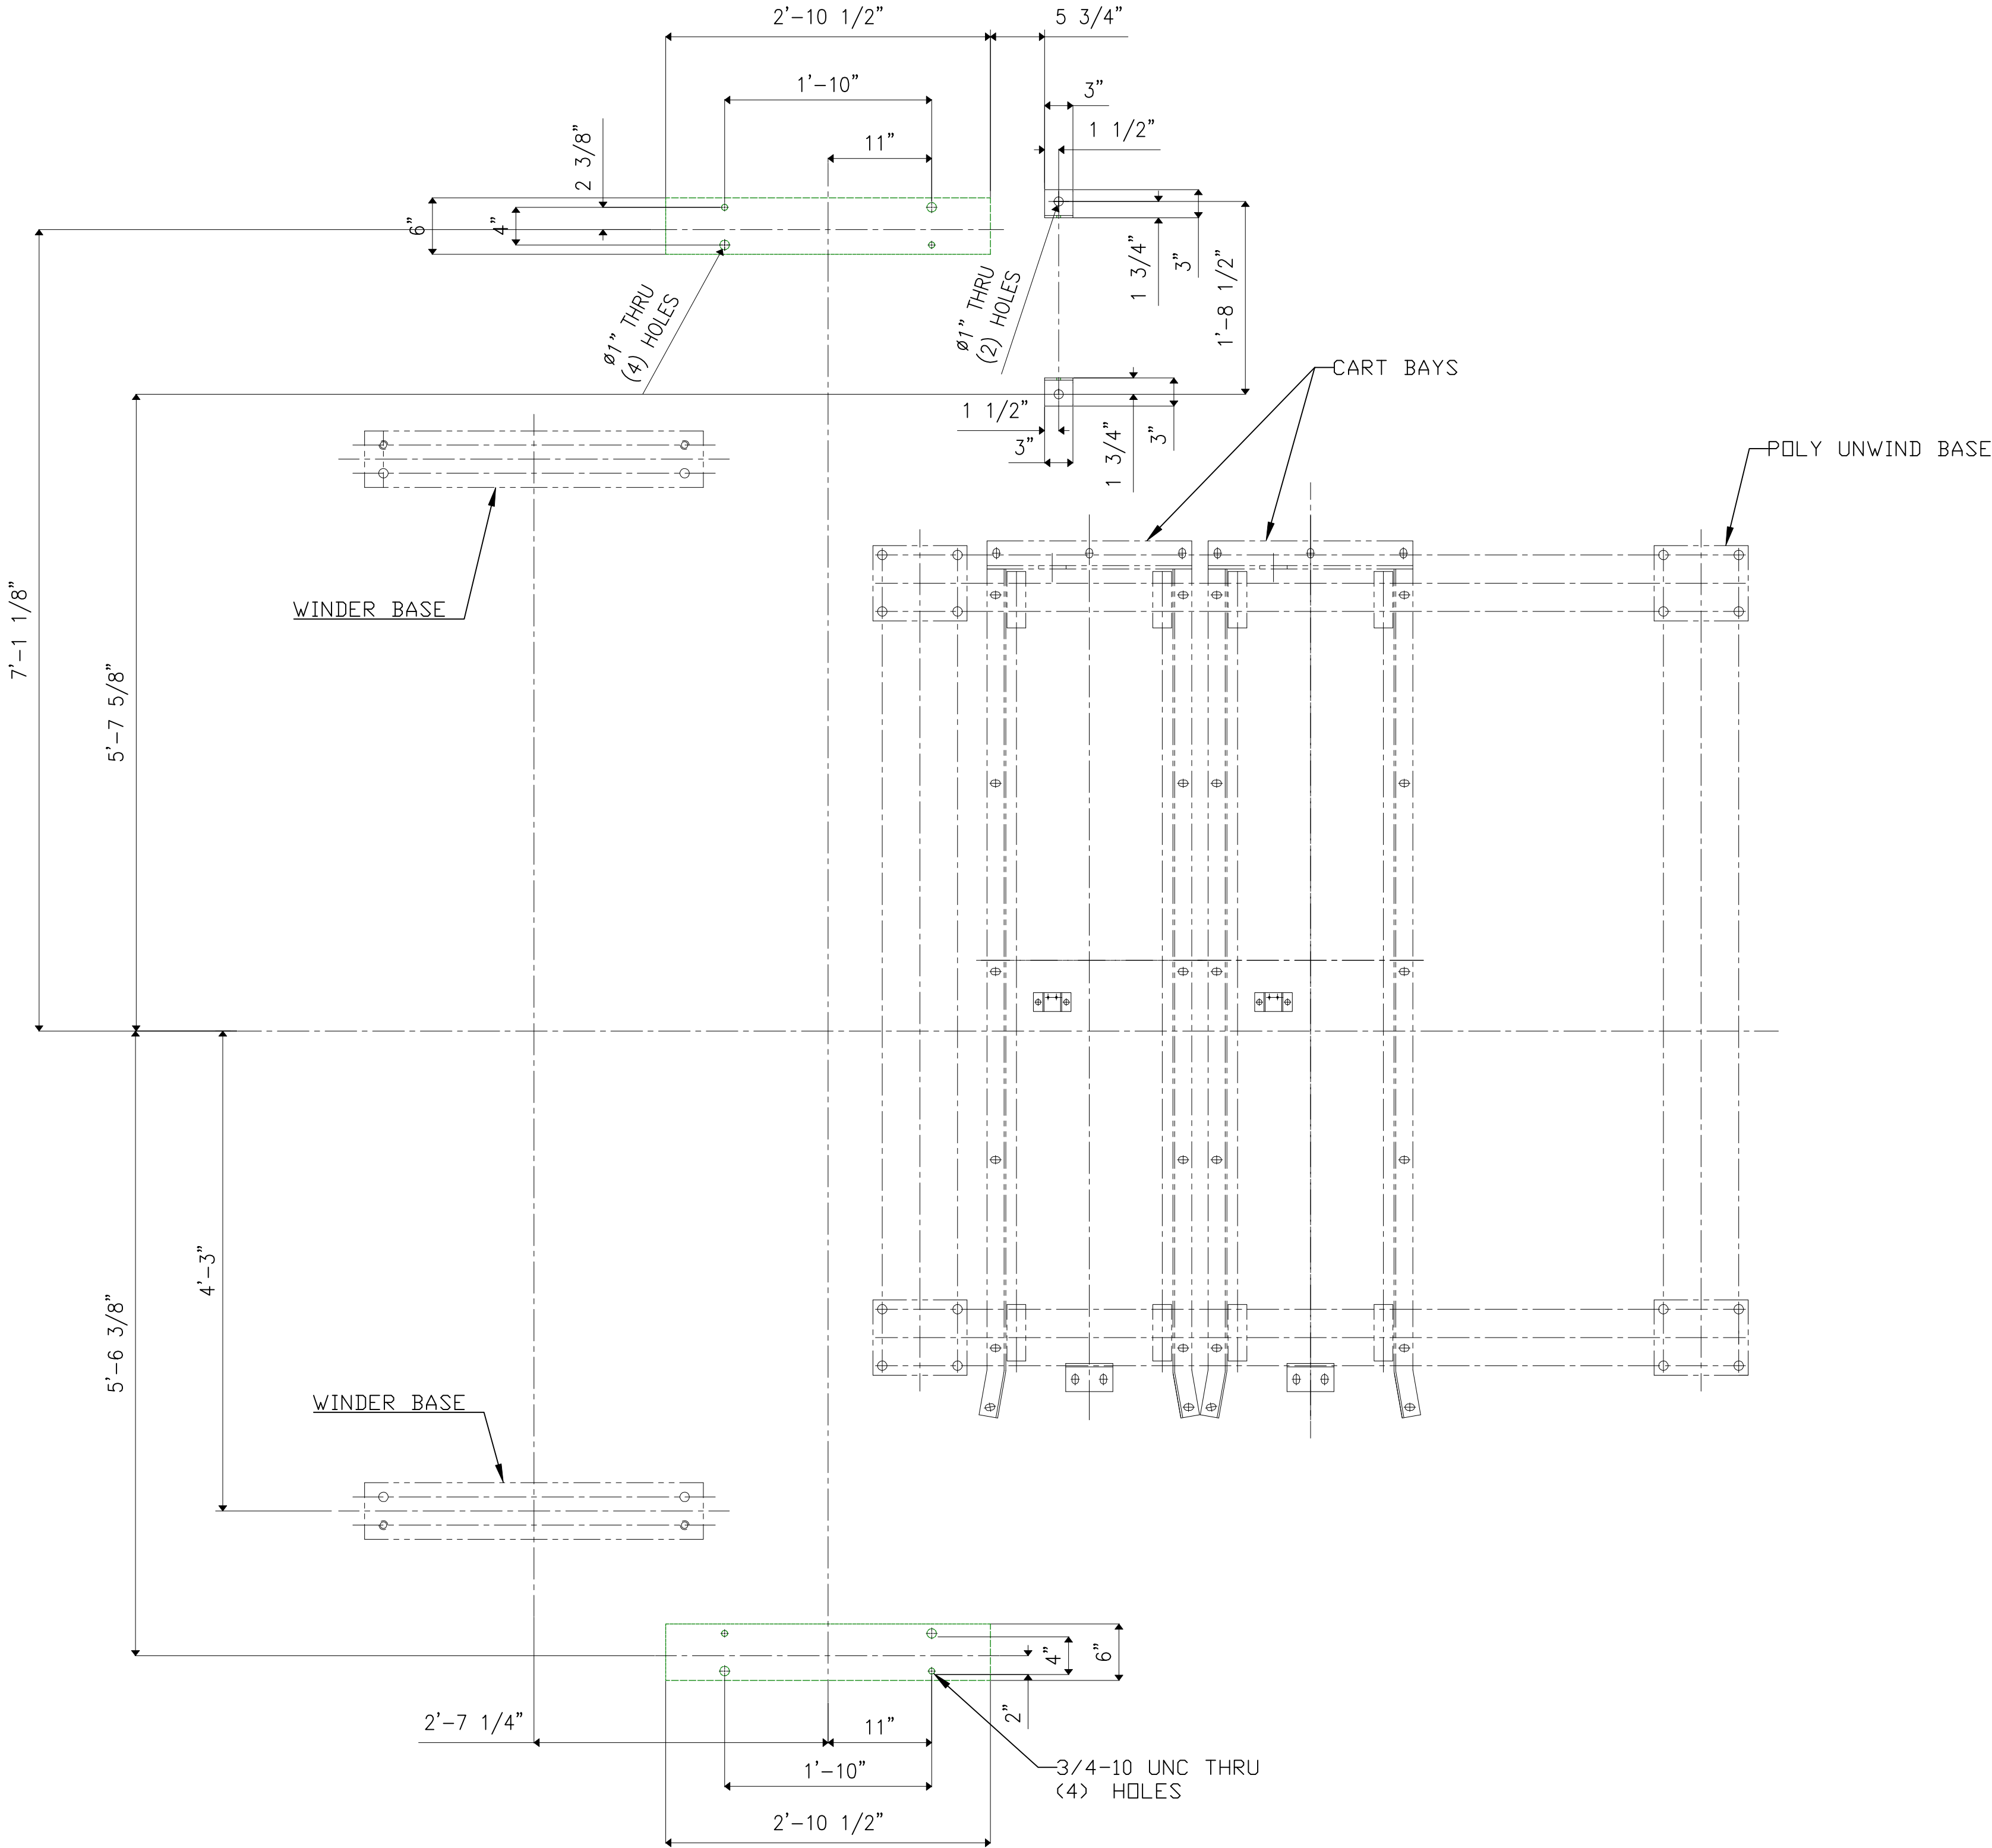

|           |                                                                        |  |                                                             |  |                                                              |  |   |  |   |   |  |   |  |   |  |                                                       |  |
|-----------|------------------------------------------------------------------------|--|-------------------------------------------------------------|--|--------------------------------------------------------------|--|---|--|---|---|--|---|--|---|--|-------------------------------------------------------|--|
| REVISIONS | <div>WAE CO.<br/><small>Not Made Properly<br/>By LITZLER</small></div> |  | <div>LITZLER<br/>AUTOMATION<br/>DRIVES &amp; CONTROLS</div> |  | <div>PSC<br/><small>RADIO FREQUENCY BY LITZLER</small></div> |  | THIS DRAWING IS THE PROPERTY OF C. A. LITZLER CO., INC. AND IS LOANED SUBJECT TO RETURN UPON DEMAND. BORROWER AGREES THAT SAME WILL NOT BE USED IN ANY WAY DETRIMENTAL TO OWNER'S INTEREST.<br><br>C. A. LITZLER CO., INC. ASSUMES NO RESPONSIBILITY, EITHER DIRECT OR INDIRECT, FOR ANY CHANGES IN ENGINEERING DESIGN, COMPLETENESS OF DESIGN, SUBSTITUTION OF MATERIALS OR SUBSTITUTION OR ALTERATION OF COMMERCIALLY SUPPLIED OR FABRICATED COMPONENTS NOT IN COMPLETE UNIFORMITY WITH ITS DRAWINGS AND INSTRUCTIONS, UNLESS SUCH DESIGN CHANGES, DELETIONS, SUBSTITUTIONS OR ALTERATIONS ARE FIRST APPROVED BY C. A. LITZLER CO., INC. IN WRITING. |  | <div>THIRD ANGLE<br/>PROJECTION</div> <div></div> <div>BREAK ALL SHARP<br/>EDGES AND CORNERS<br/>REMOVE ALL MACHINING<br/>BURRS</div> | UNLESS OTHERWISE SPECIFIED<br>ALL DIMENSIONS ARE<br>EXPRESSED IN INCHES/MILLIMETERS<br>ALLOWABLE VARIATIONS:<br>ENGLISH UNITS      METRIC UNITS<br>FRACTIONS: ±1/16"      NO DECIMALS ±1.5mm<br>DECIMALS: .005 ±.002"      DECIMALS: .X ±.05mm<br>ON METRIC ASSEMBLY DRAWINGS ROUND<br>DECIMAL DIMENSIONS TO THE NEAREST<br>WHOLE MILLIMETER |  | DRAWING APPROVAL<br><input type="checkbox"/> APPROVED AS DRAWN <input type="checkbox"/> APPROVED AS NOTED<br><br>NAME      DATE |  | <div>C. A. LITZLER CO., INC.</div> <div>CLEVELAND, OHIO 44135-2689, U.S.A. 216-267-8020 (FAX) 216-267-9856 WEBSITE: WWW.CALITZLER.COM</div> |  | JOB NUMBER: 2058    SECTION: 98.11<br>SCALE: 1"=1'-0" |  |
|           | TITLE<br>ACCUMULATOR PLATFORM AK<br>FOUNDATION                         |  | DRAWN BY<br>DPB 12/18/25                                    |  | DWG. NO.<br>DA18123 02 B                                     |  | SHEET<br>SHT. REV.   |  |   | TOTAL DRAWING SHEETS    2   |  |   |  |   |  |                                                       |  |
|           | FOR                                                                    |  | CHECKED BY<br>JLC 12/22/25                                  |  | APPROVED BY<br>RFK 12/22/25                                  |  | REF. DWG.   |  |   |   |  |   |  |   |  |                                                       |  |
|           |                                                                        |  | APPROVED BY                                                 |  |                                                              |  |   |  |   |   |  |   |  |   |  |                                                       |  |

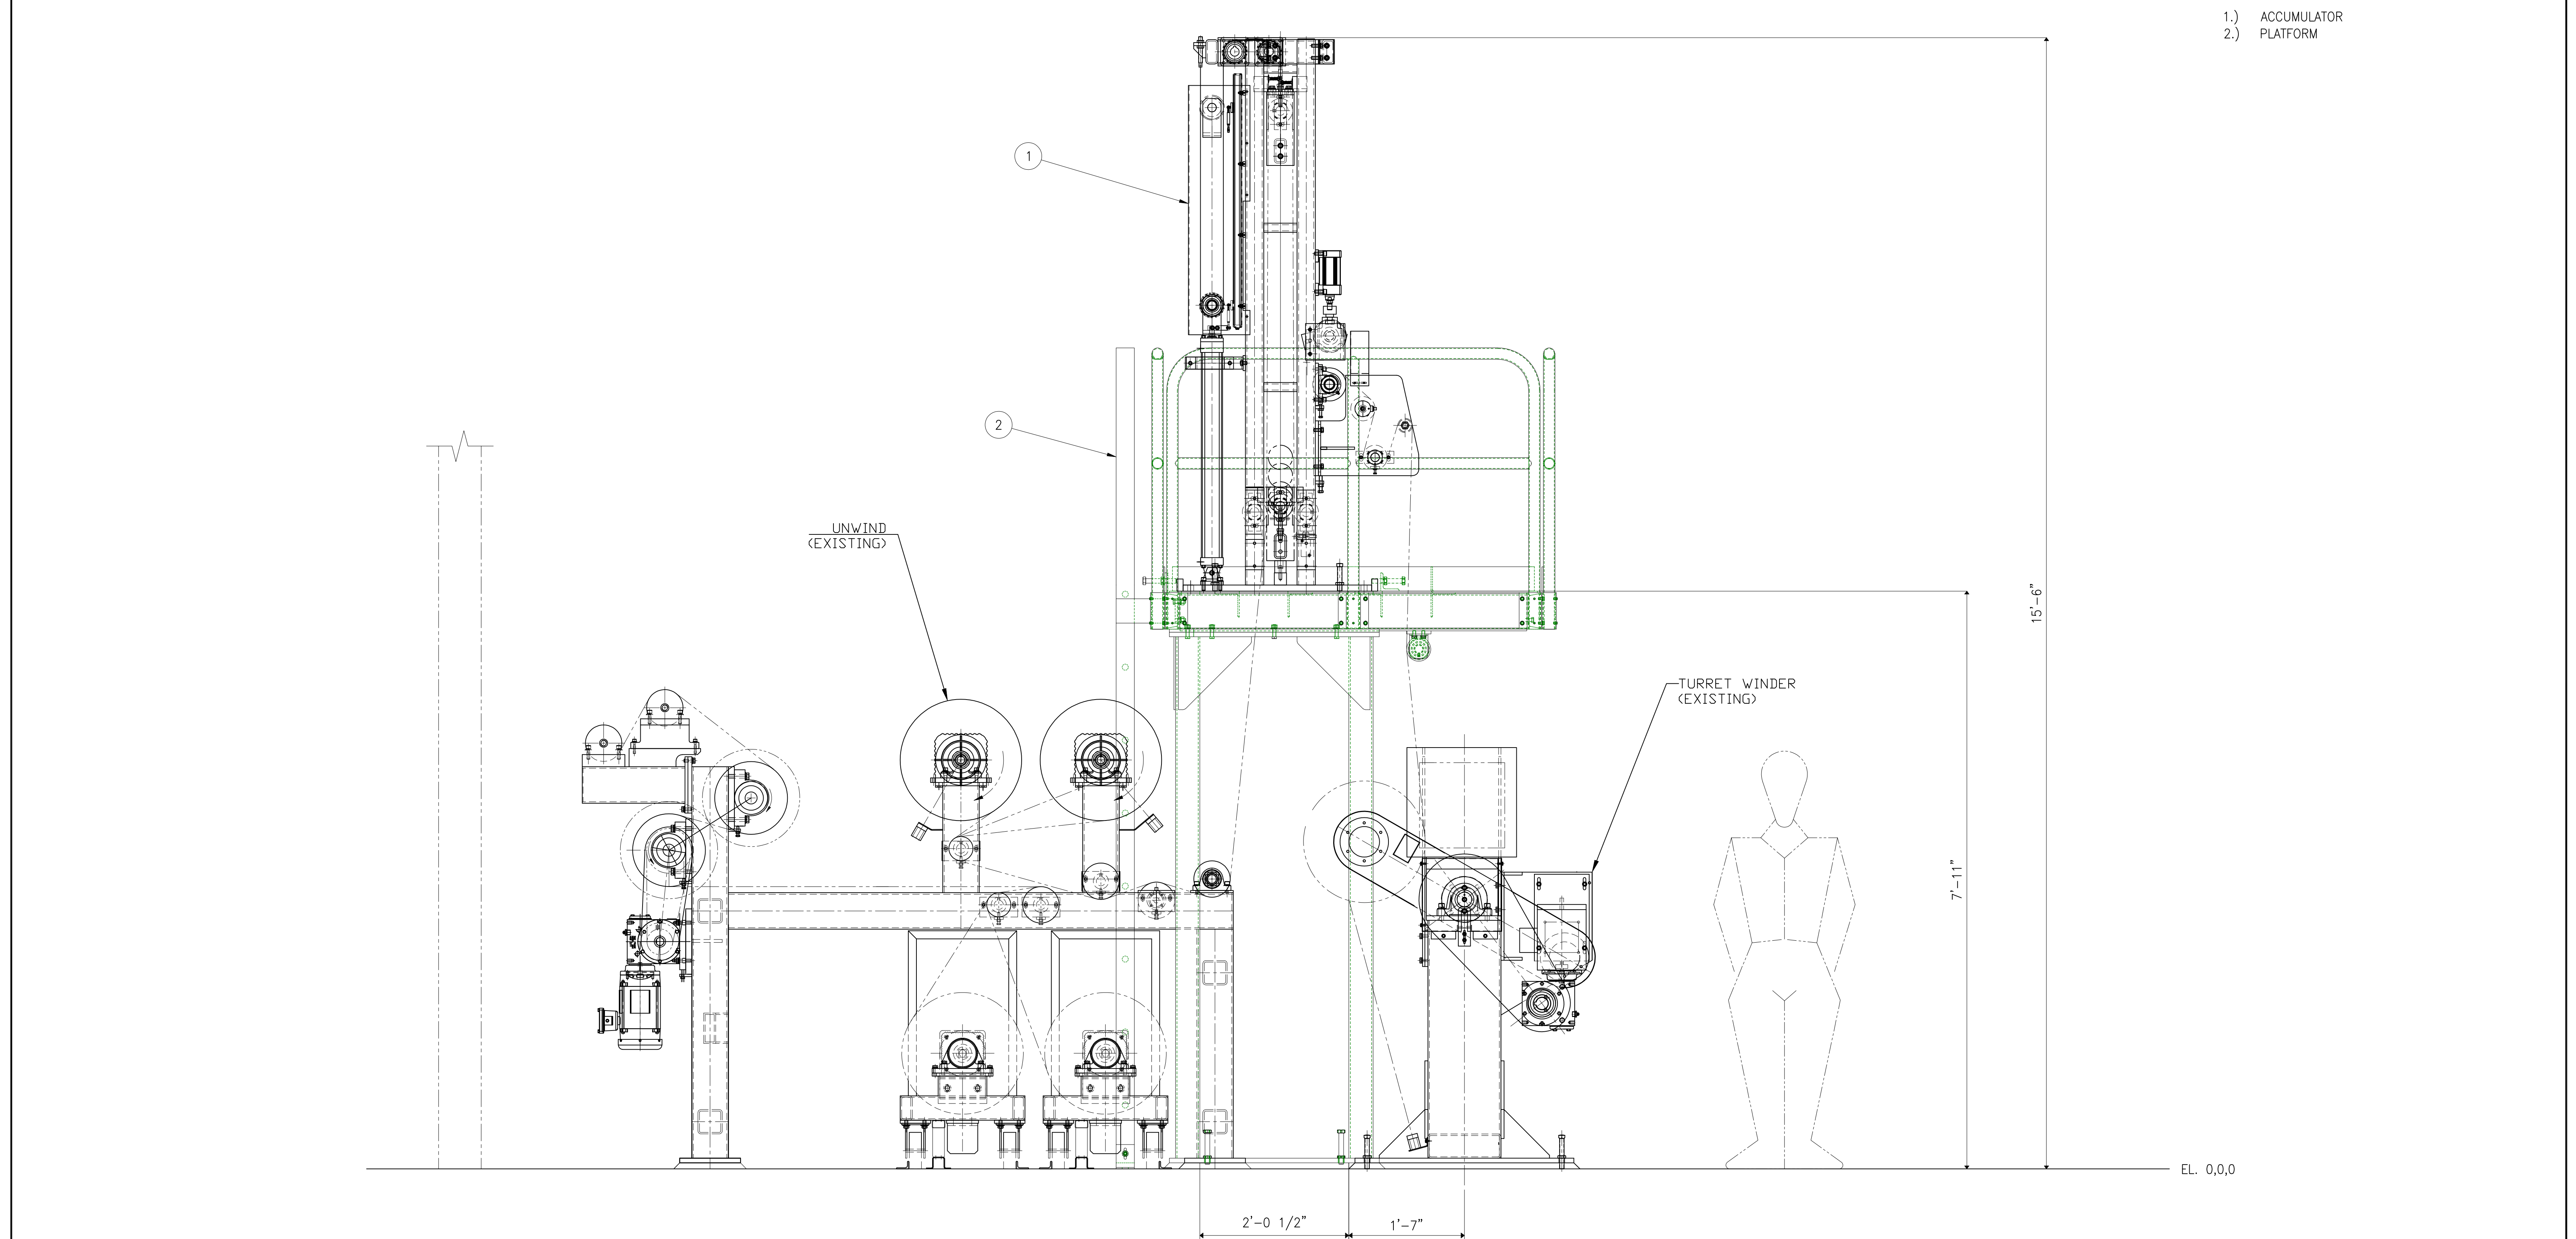

- 1.) ACCUMULATOR  
2.) PLATFORM

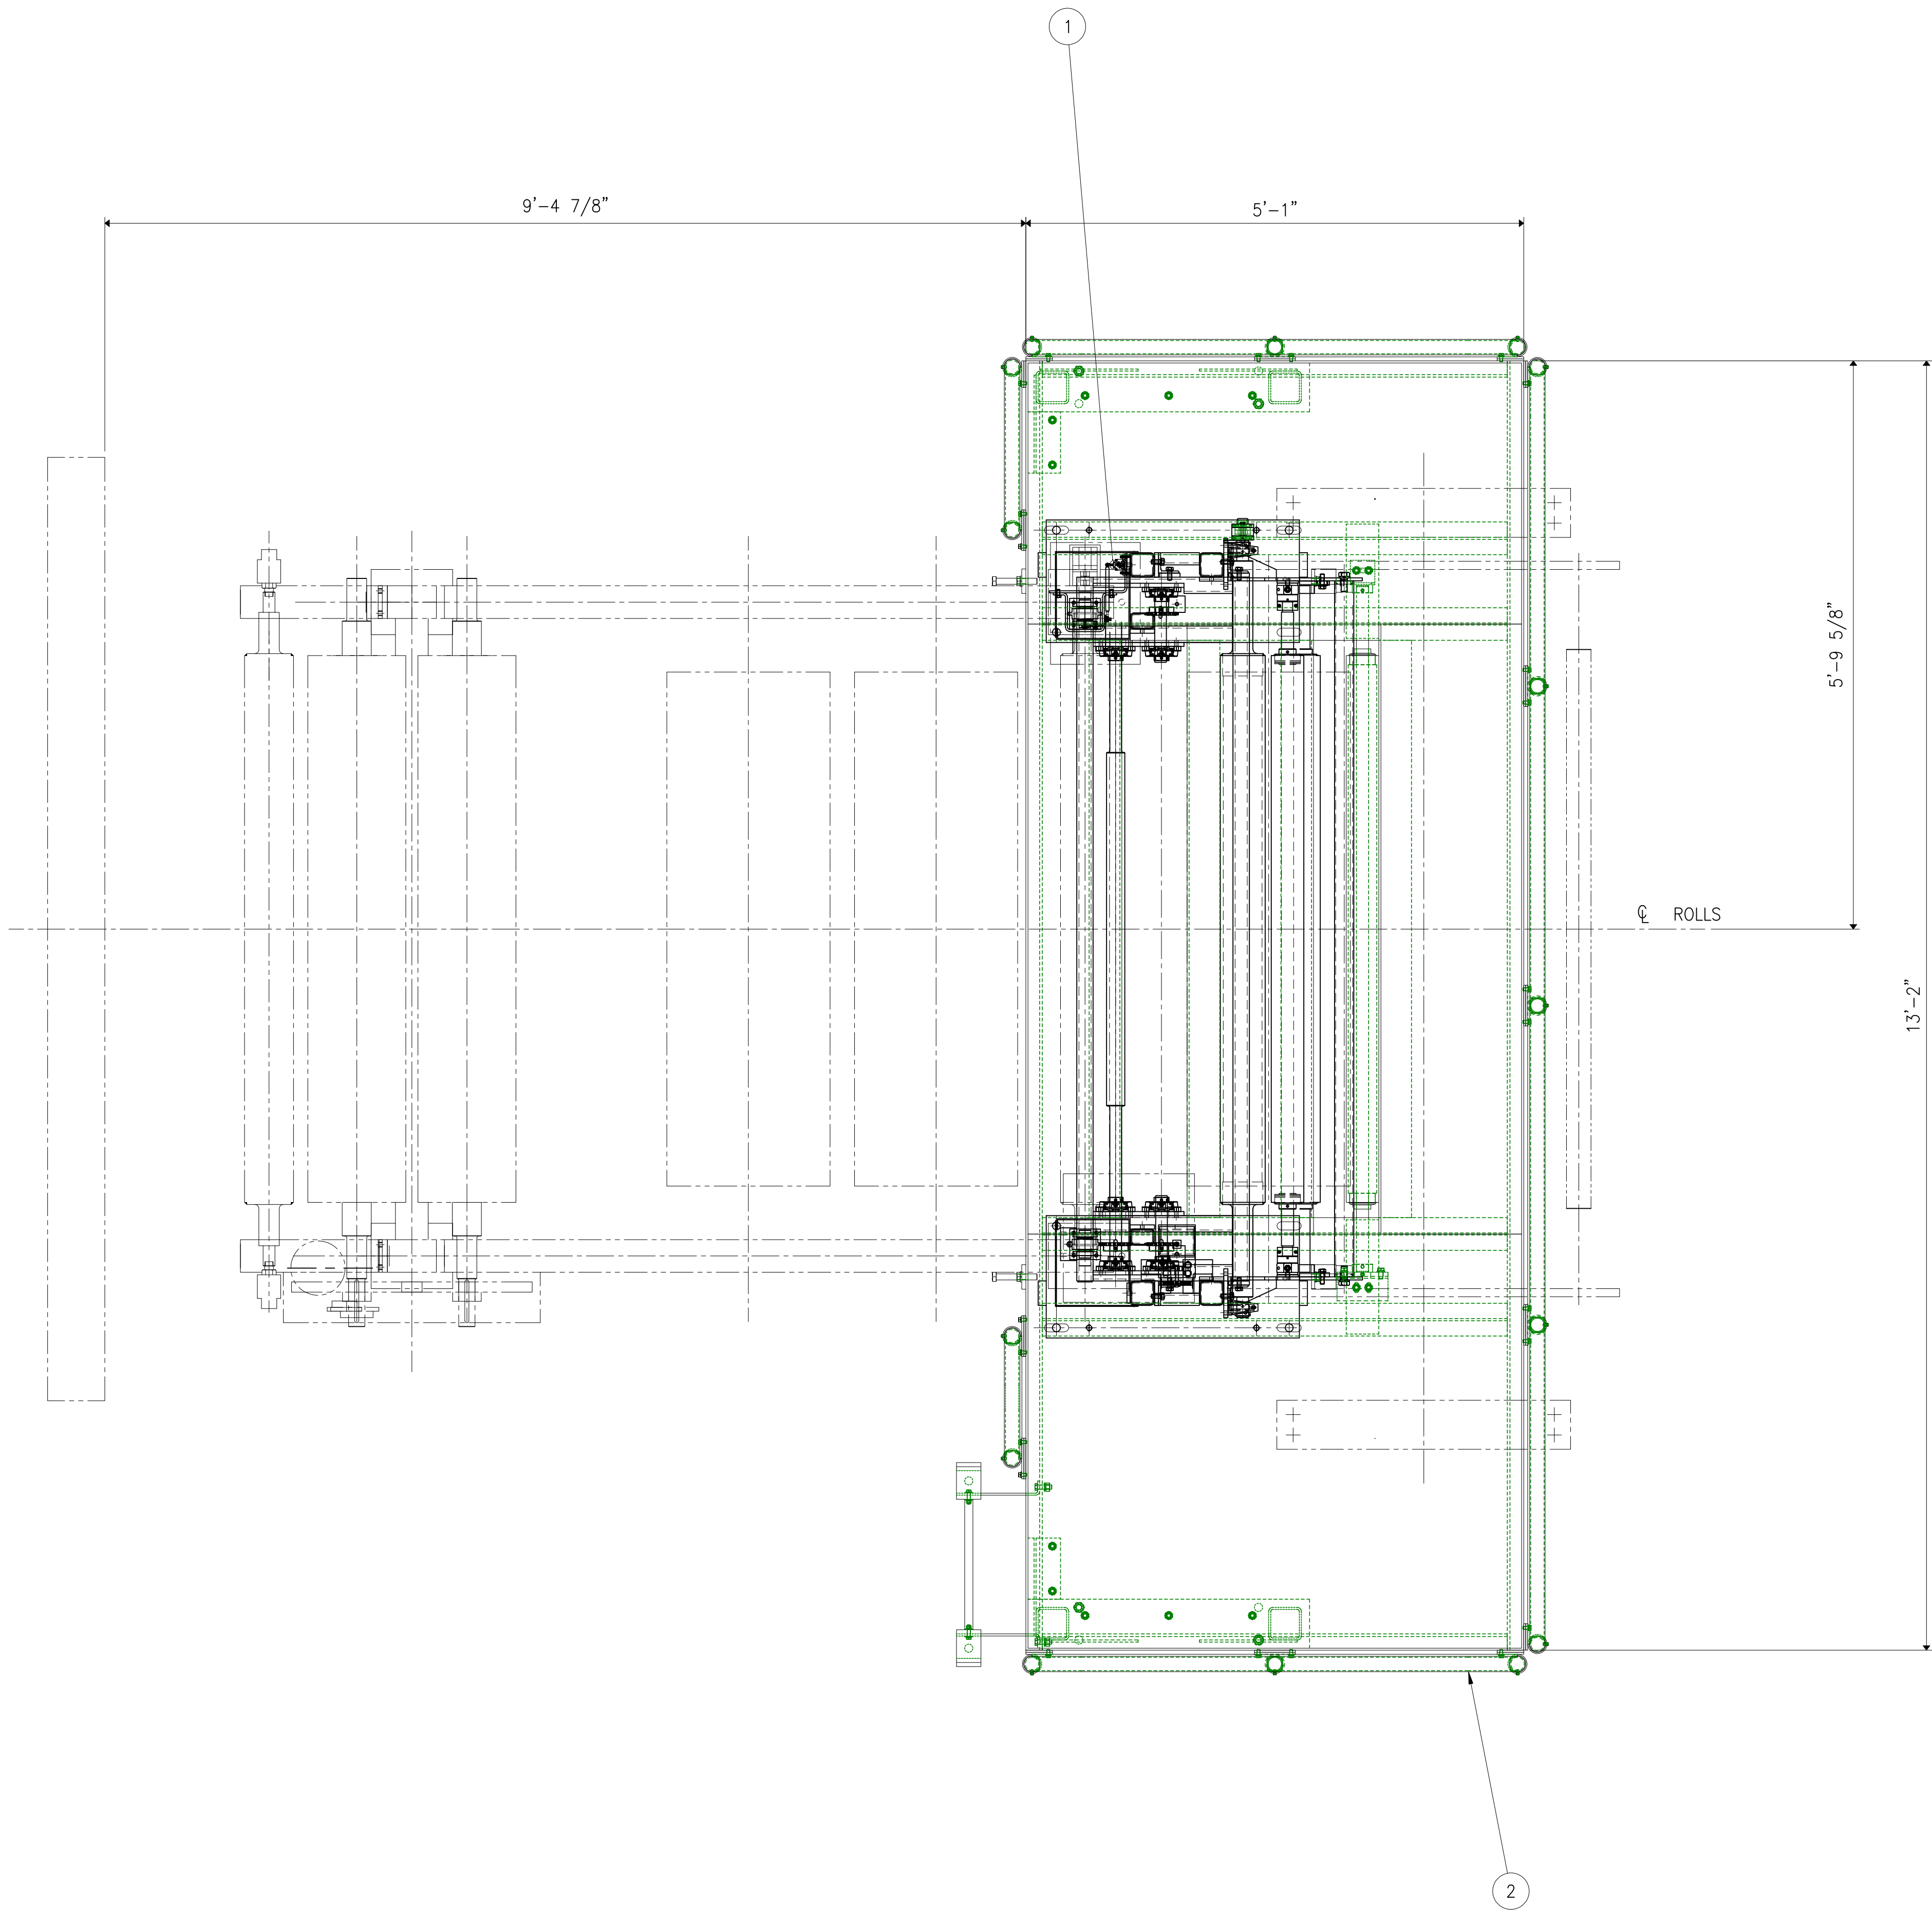


REVISIONS



THIS DRAWING IS THE PROPERTY OF C. A. LITZLER CO., INC. AND IS LOANED SUBJECT TO RETURN UPON DEMAND. BORROWER AGREES THAT SAME WILL NOT BE USED IN ANY WAY DETRIMENTAL TO OWNER'S INTEREST.

C. A. LITZLER CO., INC. ASSUMES NO RESPONSIBILITY, EITHER DIRECT OR INDIRECT, FOR ANY CHANGES IN ENGINEERING DESIGN, COMPLETENESS OF DESIGN, SUBSTITUTION OF MATERIALS OR FABRICATED COMPONENTS NOT IN COMPLETE CONFORMITY WITH ITS DRAWINGS AND INSTRUCTIONS, UNLESS SUCH DESIGN CHANGES, DELETIONS, SUBSTITUTIONS OR ALTERATIONS ARE FIRST APPROVED BY C. A. LITZLER CO., INC. IN WRITING.

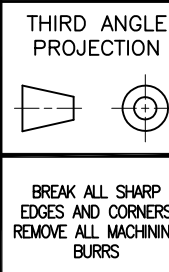

UNLESS OTHERWISE SPECIFIED

ALL DIMENSIONS ARE EXPRESSED IN INCHES/MILLIMETERS

ALLOWABLE VARIATIONS:

| ENGLISH UNITS          | METRIC UNITS                    |
|------------------------|---------------------------------|
| FRACTIONS: $\pm 1/16"$ | NO DECIMALS: $\pm 1.5\text{mm}$ |
| DECIMALS: $\pm 0.005$  | DECIMALS: $\pm 0.10\text{mm}$   |
| ANGLES: $\pm 30'$      | ANGLES: $\pm 0.5^\circ$         |

ON METRIC ASSEMBLY DRAWINGS ROUND DECIMAL DIMENSIONS TO THE NEAREST WHOLE MILLIMETER.

DRAWING APPROVAL

☐ APPROVED AS DRAWN ☐ APPROVED AS NOTED

NAME \_\_\_\_\_ DATE \_\_\_\_\_

**C. A. LITZLER CO., INC.**  
CLEVELAND, OHIO 44135-2689, U.S.A. 216-267-8020 (FAX) 216-267-9856 WEBSITE: WWW.CALITZLER.COM

| TITLE           | DRAWN BY     | CHECKED BY   | APPROVED BY  |
|-----------------|--------------|--------------|--------------|
| GENERAL LINE AJ | DPB 12/22/25 | JLC 12/22/25 | RFK 12/22/25 |


JOB NUMBER: 2058 SECTION: 98.22

SCALE: 1"=1'-0"



DWG. NO. **DA18126 02 B**

TOTAL DRAWING SHEETS 4

REF. DWG.

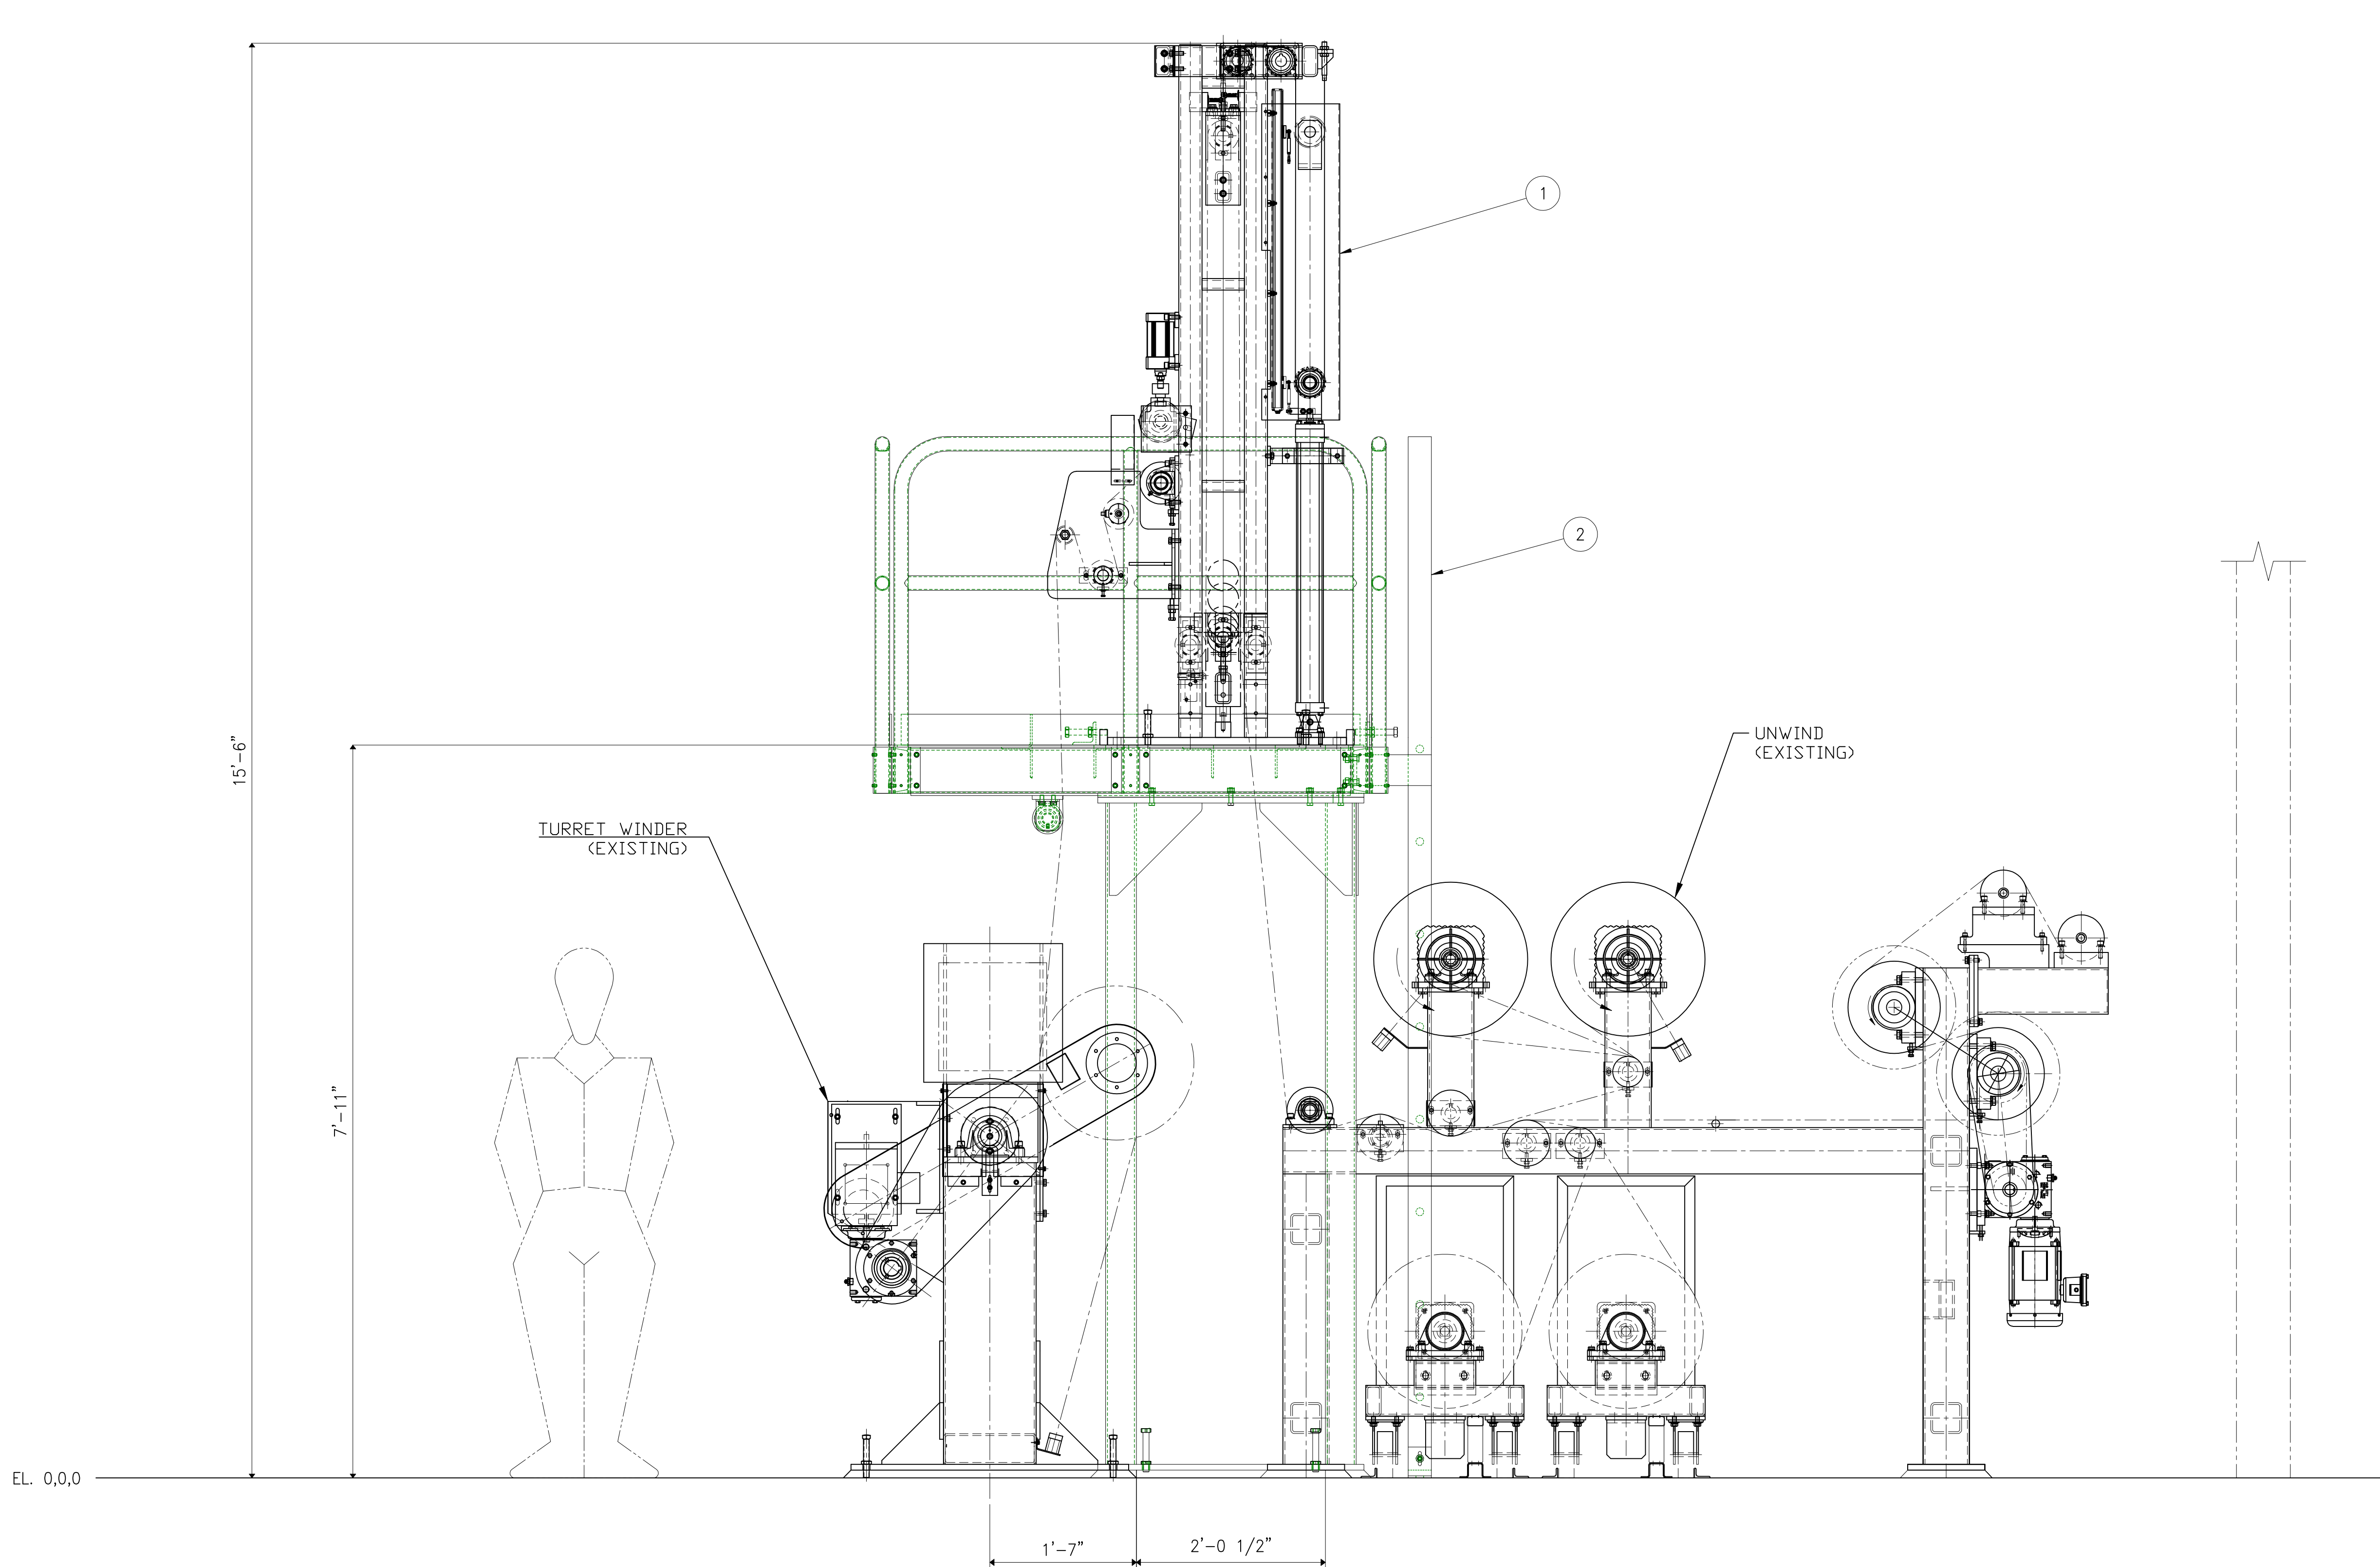

REVISIONS

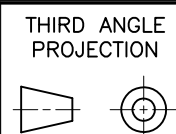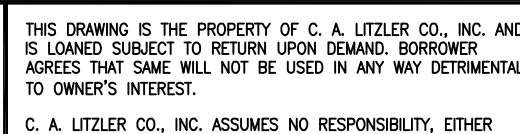

| UNLESS OTHERWISE SPECIFIED                                                           |                      |
|--------------------------------------------------------------------------------------|----------------------|
| ALL DIMENSIONS ARE EXPRESSED IN INCHES/MILLIMETERS                                   |                      |
| ALLOWABLE VARIATIONS:                                                                |                      |
| ENGLISH UNITS                                                                        | METRIC UNITS         |
| FRACTIONS: 1/16"                                                                     | NO DECIMALS: ±1.5mm  |
| DECIMALS: .XX = ±.02"                                                                | DECIMALS: X = ±0.5mm |
| XXX = ±.001                                                                          | XX = ±.01mm          |
| ANGLES: 1/2°-30°                                                                     |                      |
| ON METRIC ASSEMBLY DRAWINGS ROUND DECIMAL DIMENSIONS TO THE NEAREST WHOLE MILLIMETER |                      |


| DRAWING APPROVAL                           |                                            |
|--------------------------------------------|--------------------------------------------|
| <input type="checkbox"/> APPROVED AS DRAWN | <input type="checkbox"/> APPROVED AS NOTED |
| NAME                                       | DATE                                       |

| C. A. LITZLER CO., INC.                                                                       |                 |             |              |
|-----------------------------------------------------------------------------------------------|-----------------|-------------|--------------|
| CLEVELAND, OHIO 44135-2689, U.S.A. 216-267-8020 (FAX) 216-267-9856 WEBSITE: WWW.CALITZLER.COM |                 |             |              |
| TITLE                                                                                         | GENERAL LINE AK | DRAWN BY    | DPB 12/19/25 |
| CHECKED BY                                                                                    | JLC 12/23/25    | APPROVED BY | RFK 12/23/25 |
| FOR                                                                                           |                 | APPROVED BY | RFK 12/23/25 |

|                        |                       |
|------------------------|-----------------------|
| JOB NUMBER: 2058       | SECTION: 98.22        |
| SCALE: 1"=1'-0"        | DWG. NO. DA18126 03 B |
| TOTAL DRAWING SHEETS 4 | SHT. REV.             |

REF. DWG.

- 1.) ACCUMULATOR  
2.) PLATFORM

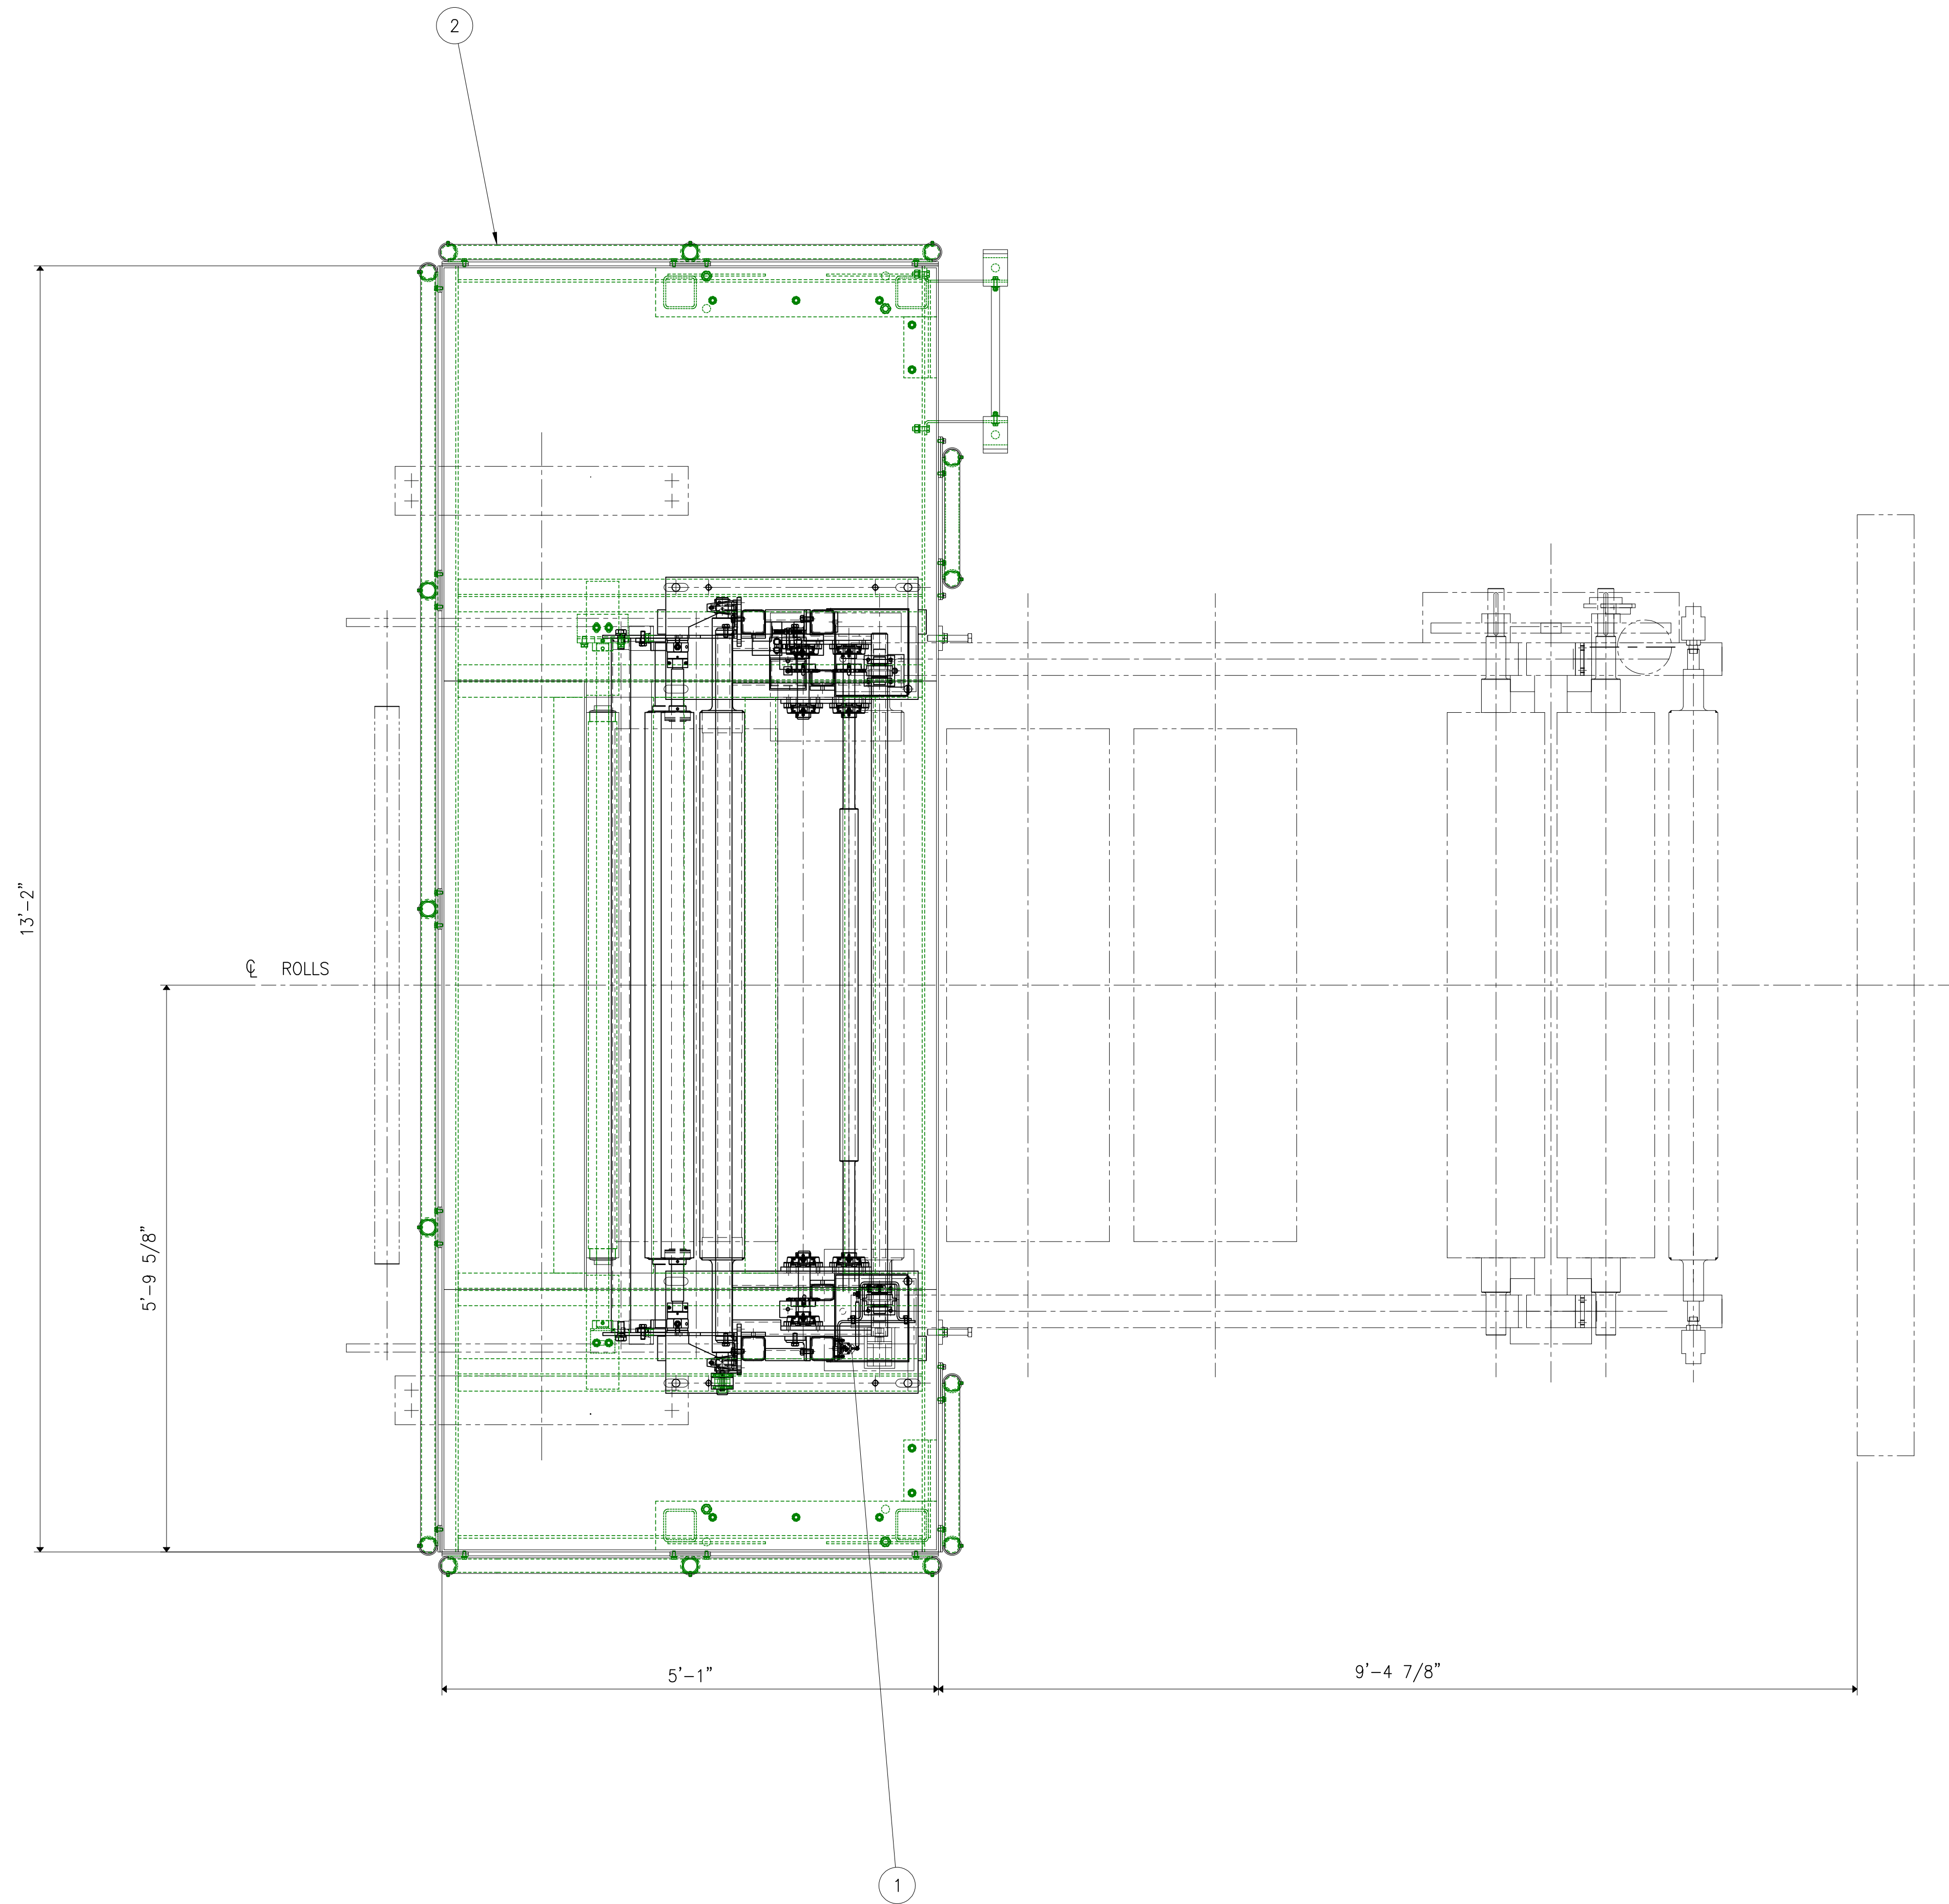


REVISIONS



THIS DRAWING IS THE PROPERTY OF C. A. LITZLER CO., INC. AND IS LOANED SUBJECT TO RETURN UPON DEMAND. BORROWER AGREES THAT SAME WILL NOT BE USED IN ANY WAY DETRIMENTAL TO OWNER'S INTEREST.

C. A. LITZLER CO., INC. ASSUMES NO RESPONSIBILITY, EITHER DIRECT OR INDIRECT, FOR ANY CHANGES IN ENGINEERING DESIGN, COMPLETENESS OF DESIGN, SUBSTITUTION OF MATERIALS OR SUBSTITUTION OF ALTERNATION OF COMMERCIALLY SUPPLIED OR FABRICATED COMPONENTS NOT IN COMPLETE CONFORMITY WITH ITS DRAWINGS AND INSTRUCTIONS, UNLESS SUCH DESIGN CHANGES, DELETIONS, SUBSTITUTIONS OR ALTERATIONS ARE FIRST APPROVED BY C. A. LITZLER CO., INC. IN WRITING.

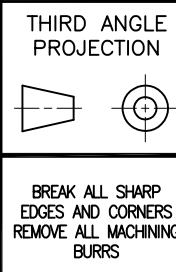

| UNLESS OTHERWISE SPECIFIED                                                            |                                 |
|---------------------------------------------------------------------------------------|---------------------------------|
| ALL DIMENSIONS ARE EXPRESSED IN INCHES/MILLIMETERS                                    |                                 |
| ALLOWABLE VARIATIONS:                                                                 |                                 |
| ENGLISH UNITS                                                                         | METRIC UNITS                    |
| FRACTIONS: $\pm 1/16"$                                                                | NO DECIMALS: $\pm 1.5\text{mm}$ |
| DECIMALS: $\pm 0.005"$                                                                | DECIMALS: $\pm 0.10\text{mm}$   |
| ANGLES: $\pm 30'$                                                                     | ANGLES: $\pm 0.5^\circ$         |
| ON METRIC ASSEMBLY DRAWINGS ROUND DECIMAL DIMENSIONS TO THE NEAREST WHOLE MILLIMETER. |                                 |

DRAWING APPROVAL

☐ APPROVED AS DRAWN ☐ APPROVED AS NOTED

NAME

DATE

C. A. LITZLER CO., INC.

CLEVELAND, OHIO 44135-2689, U.S.A. 216-267-8020 (FAX) 216-267-9856 WEBSITE: WWW.CALITZLER.COM

TITLE GENERAL LINE AJ

FOR

DRAWN BY DPB 12/22/25

CHECKED BY JLC 12/23/25

APPROVED BY RFK 12/23/25

JOB NUMBER: 2058 SECTION: 98.22

SCALE: 1"=1'-0"

DWG. NO. DA18126 04 B

SHT. REV.

TOTAL DRAWING SHEETS 4

REF. DWG.