

PRODUCT:

MATERIAL: WOVEN GLASS/CARBON FIBER ARAMIDS
WIDTH: 63" MAXIMUM

UTILITIES:

ELECTRIC POWER: 480 VAC, 3 PHASE, 60 Hz
ELECTRIC CONTROL: 24 VDC

COMPRESSED AIR: 80 PSI, CLEAN, DRY

CODE:

INSURANCE CODE: FM GLOBAL
OVEN CODE: NFPA 86
ELECTRICAL CODE: NEC
STEEL CODE: AISC
SAFETY CODE: OSHA, ASME
SEISMIC CODE: IBC

MACHINE:


LINE SPEED: 5-30 FPM

TENSIONS: 1.0 PLI TO 2.5 PLI

NIP ROLLS: ROLL DIA.: UPPER Ø5 1/2" WITH 9/16" HYPALON 75 SHORE A DUROMETER
LOWER Ø5 1/2" WITH STEEL CHROME PLATED
ROLL FACE: 67"

IDLER ROLLS: ROLL DIA.: Ø4" ANODIZED ALUMINUM
ROLL FACE: 67"

STORAGE: 26 SECONDS @ 23 FPM (MORE AT LOWER SPEEDS)

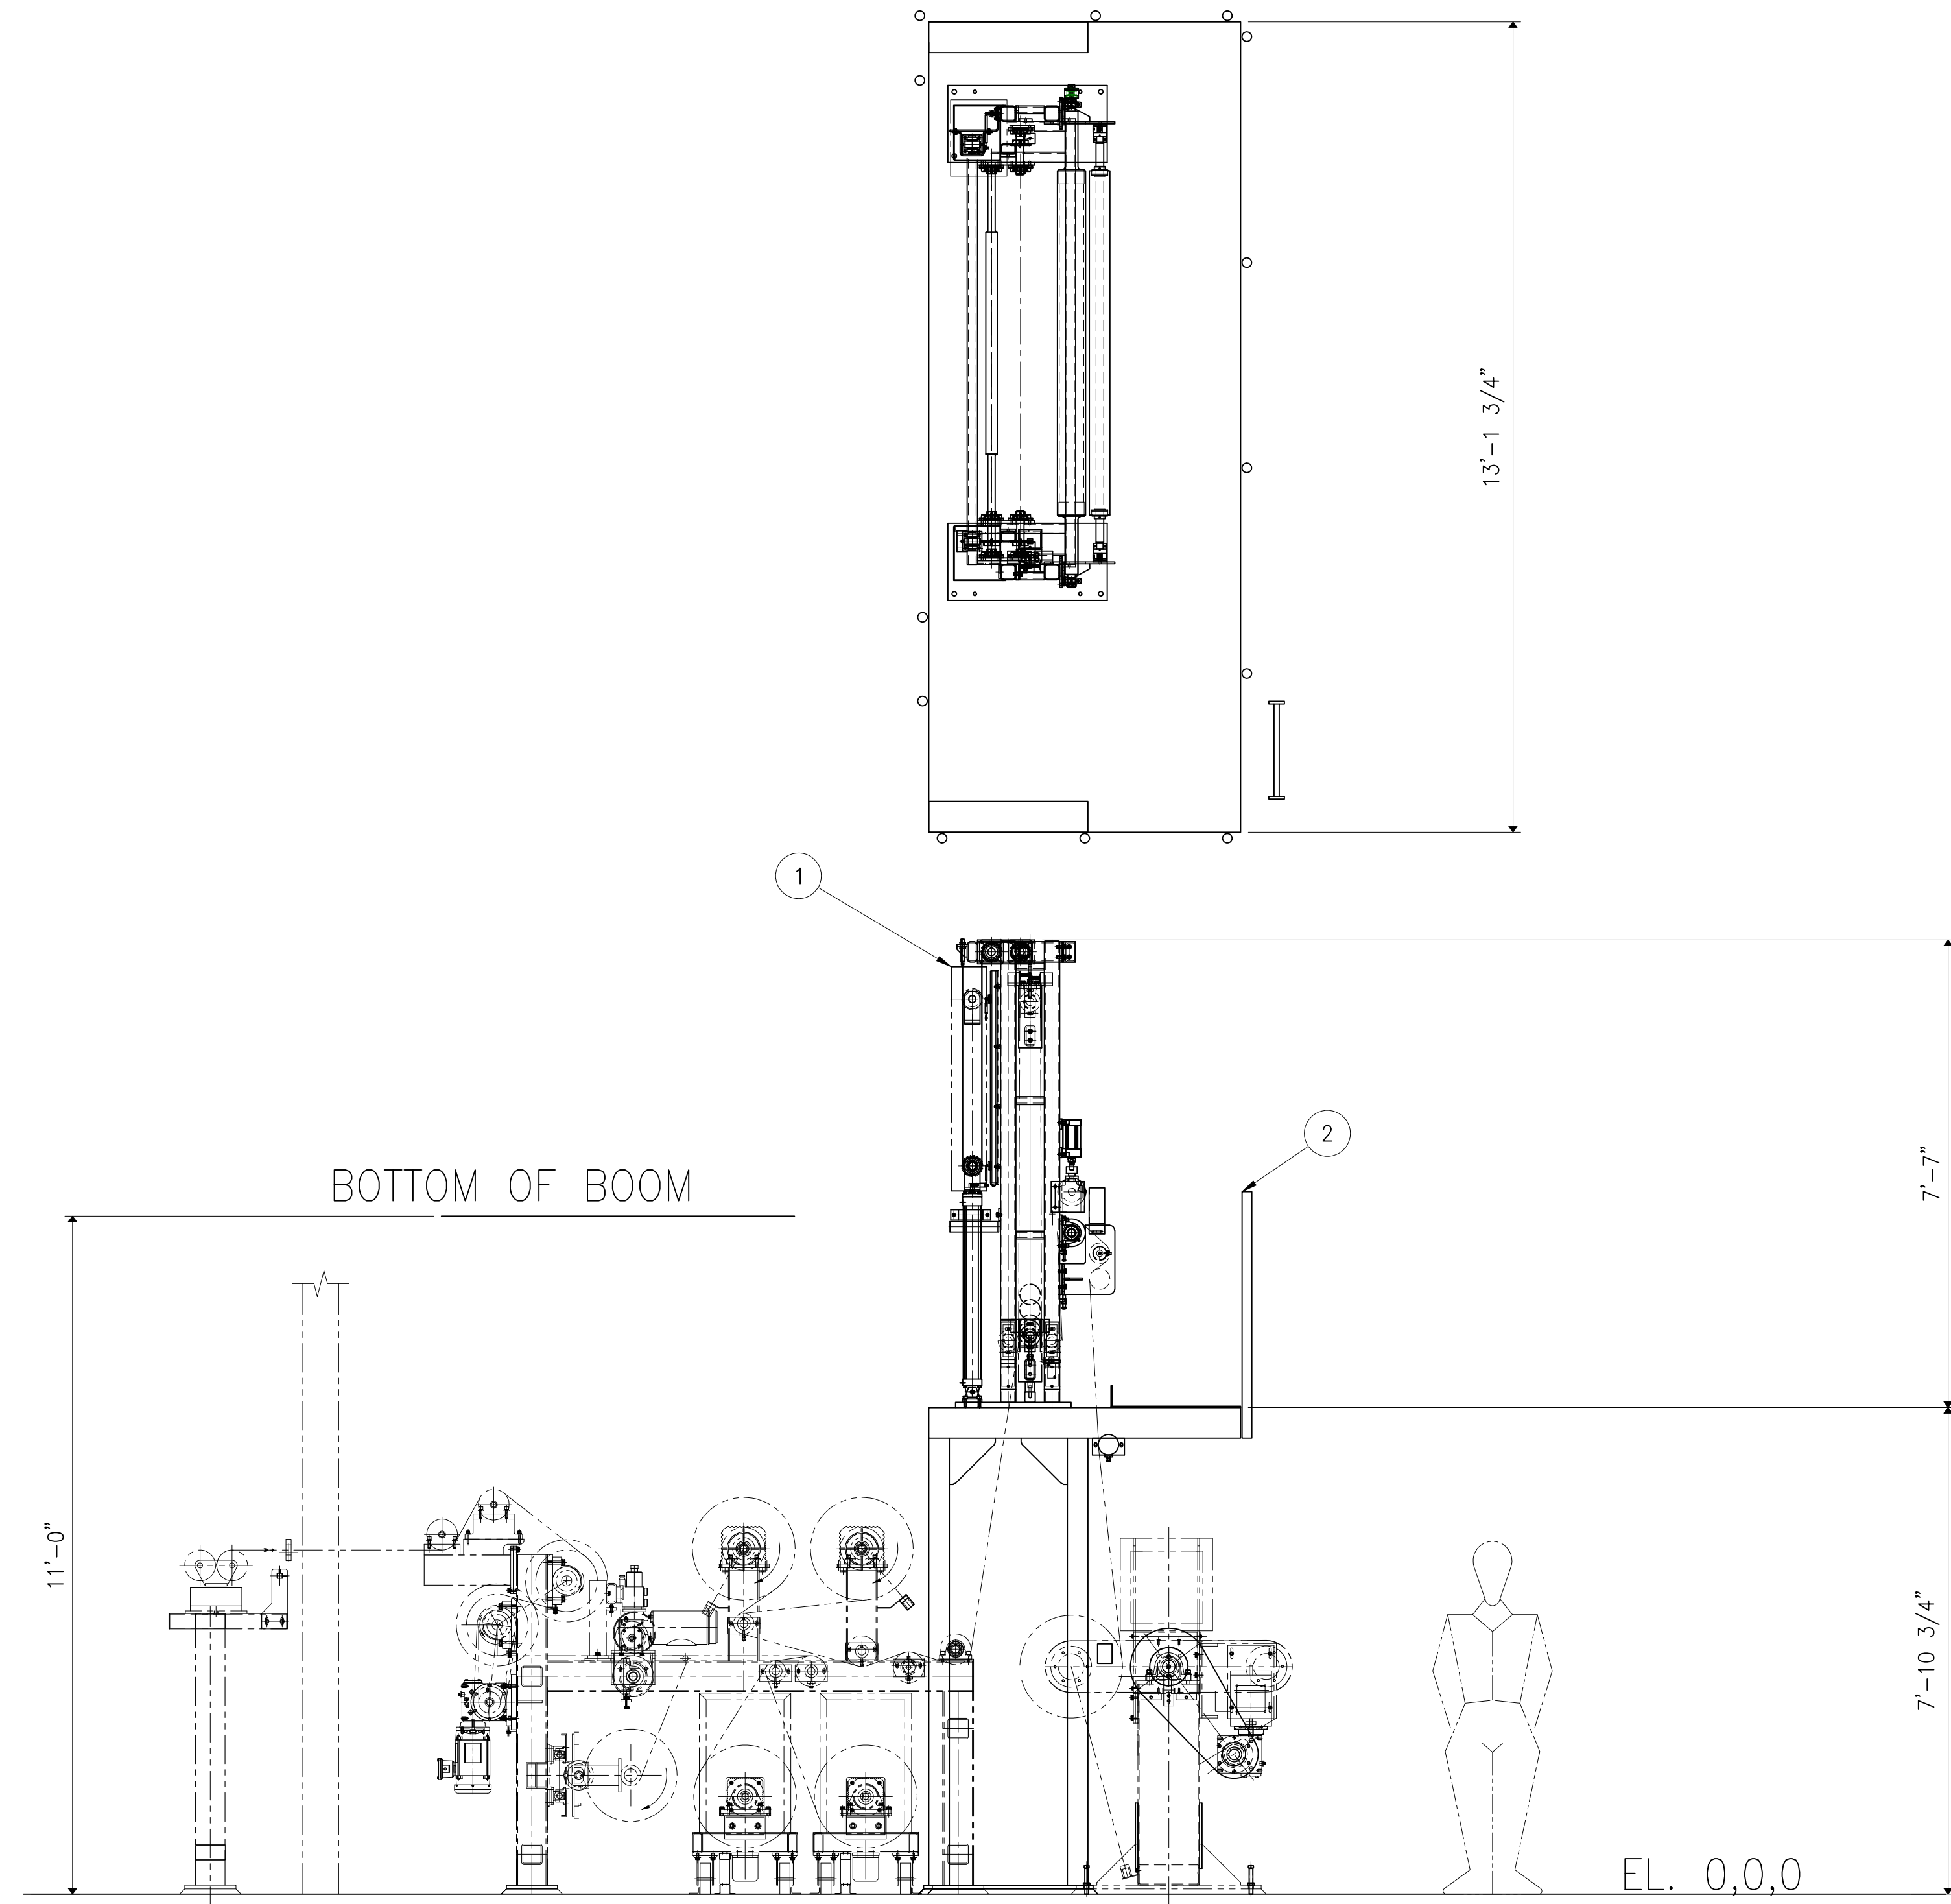


1. ACCUMULATOR AJ/AK
2. PLATFORM

REVISIONS



THIS DRAWING IS THE PROPERTY OF C. A. LITZLER CO., INC. AND IS LOANED SUBJECT TO RETURN UPON DEMAND. BORROWER AGREES THAT SAME WILL NOT BE USED IN ANY WAY DETRIMENTAL TO OWNER'S INTEREST.
C. A. LITZLER CO., INC. ASSUMES NO RESPONSIBILITY, EITHER DIRECT OR INDIRECT, FOR ANY CHANGES IN ENGINEERING DESIGN, COMPLETENESS OF DESIGN, SUBSTITUTION OF MATERIALS OR SUBSTITUTION OR ALTERATION OF COMMERCIALY SUPPLIED OR FABRICATED COMPONENTS NOT IN COMPLETE UNIFORMITY WITH IT'S DRAWINGS AND INSTRUCTIONS, UNLESS SUCH DESIGN CHANGES, DELETIONS, SUBSTITUTIONS OR ALTERATIONS ARE FIRST APPROVED BY C. A. LITZLER CO., INC. IN WRITING.

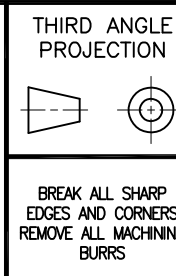

UNLESS OTHERWISE SPECIFIED	
ALL DIMENSIONS ARE EXPRESSED IN INCHES/MILLIMETERS	
ALLOWABLE VARIATIONS:	
ENGLISH UNITS	METRIC UNITS
FRACTIONS: $\pm 1/16"$	NO DECIMALS: ± 1.5
DECIMALS: $.XX = \pm .02"$ $.XXX = \pm .005"$	DECIMALS: $X = \pm 0.5$ $.XX = \pm 0.1$
ANGLES: $\pm 0^\circ - 30^\circ$	
ON METRIC ASSEMBLY DRAWINGS ROUND DECIMAL DIMENSIONS TO THE NEAREST WHOLE MILLIMETER	

DRAWING APPROVAL	
☐ APPROVED AS DRAWN	☐ APPROVED AS NOTED
NAME	DATE

C. A. LITZLER CO., INC.			
CLEVELAND, OHIO 44135-2689, U.S.A. 216-267-8020 (FAX) 216-267-9856 WEBSITE: WWW.CALITZLER.COM			
TITLE	DESIGN INFORMATION DOCUMENT	DRAWN BY	JLC
CHECKED BY		APPROVED BY	
FOR	WINDER ACCUMULATORS AJ/AK	APPROVED BY	

JOB NUMBER: 2058	SECTION: 98.24
SCALE: 1/2"=1'-0"	DWG. NO. DID2058 01 A
TOTAL DRAWING SHEETS 3	SHT. REV.





REF. DWG.

POWER & TRANSMISSION

PT1		MOTOR
PT2		VARIABLE SPEED MOTOR
PT3		GEAR REDUCER
PT4		BRAKE
PT5		CLUTCH
PT6		SAFETY CHUCK
PT7		LITZLER SAFETY CHUCK SIZE M
PT8		LITZLER SAFETY CHUCK SIZE ML
PT9		DRIVEN ROLL
PT10		AIR SHAFT
PT11		GEAR MOTOR
PT12		MAGNETIC PARTICLE BRAKE
PT13		SERVO MOTOR
PT14		FLEXIBLE DUCT
PT15		SPROCKET WITH CHAIN
PT16		HAND WHEEL
PT17		BALL SCREW
PT18		LINEAR BEARING
PT19		GEAR RACK

FLUID POWER

FP1		PUMP
FP2		PUMP VARIABLE VOLUME PRESSURE COMPENSATED
FP3		CHECK VALVE
FP4		SOLENOID VALVE (2 WAY N.O.)
FP5		SOLENOID VALVE (2 WAY N.C.)
FP6		MANUAL VALVE (3 WAY)
FP7		SOLENOID VALVE (3 WAY N.O.)
FP8		SOLENOID VALVE (3 WAY N.C.)
FP9		MANUAL VALVE (4 WAY)
FP10		SOLENOID VALVE (4 WAY)
FP11		MANUAL VALVE
FP12		SAFETY SHUTOFF VALVE (LOCKABLE)
FP13		PRESSURE OPERATED VALVE
FP14		PRESSURE REDUCING RELIEVING VALVE
FP15		CONTROL VALVE
FP16		HOSE
FP17		LUBRICATOR
FP18		MUFFLER
FP19		QUICK DISCONNECT
FP20		FILTER
FP21		PRESSURE GAUGE
FP22		SPEED CONTROL
FP23		REGULATOR
FP24		REGULATOR W/ GAUGE
FP25		PILOT OPERATED REGULATOR
FP26		PNEUMATIC OPERATOR
FP27		PNEUMATIC OPERATOR WITH PNEUMATIC POSITIONER
FP28		PNEUMATIC OPERATOR WITH ELECTRO/PNEUMATIC POSITIONER

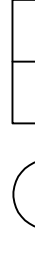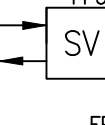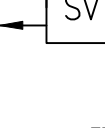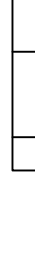FP29		AIR CYLINDER (SINGLE ACTING SPRING RETURN)
FP30		AIR CYLINDER (DOUBLE ACTING)
FP31		NIP
FP32		FLACK PACK
FP33		AIR MOTOR
FP34		RETRACTING AIR HOSE
FP35		RETRACTING AIR HOSE
FP36		SOLENOID VALVE (5 WAY 1 INLET)
FP37		SOLENOID VALVE (5 WAY 2 INLET)
FP38		AIR CYLINDER W. ROD LOCK (DOUBLE ACTING)
P39		LOW PRESSURE RELIEVING VALVE

INPUT SENSOR

IS1		LIMIT SWITCH
IS2		PRESSURE SWITCH
IS3		DIFFERENTIAL PRESSURE SWITCH
IS4		PRESSURE TRANSMITTER
IS5		DIFFERENTIAL PRESSURE TRANSMITTER
IS6		LINEAR POSITION TRANSMITTER
IS7		POSITION TRANSMITTER
IS8		SPLICE DETECTOR
IS9		COUNTER LOCAL READOUT
IS10		COUNTER REMOTE READOUT
IS11		UV DETECTOR
IS12		LEL SENSOR
IS13		PHOTO CELL
IS14		THERMOCOUPLE
IS15		DIFFERENTIAL PRESSURE GAUGE
IS16		TEMPERATURE ACTIVATED SWITCH
IS17		PROXIMITY SWITCH
IS18		RESISTANCE TEMPERATURE DETECTOR
IS19		PHOTO EYE

OUTPUT CONTROL

OC1		E-STOP
OC2		SPARK IGNITOR
OC3		ACTUATOR ELECTRIC
OC4		FOOT SWITCH
OC5		ELECTRIC TO PRESSURE CONVERTER
OC6		CURRENT TO PRESSURE CONVERTER
OC7		TEMPERATURE INDICATING CONTROLLER
OC8		ENCODER
OC9		INTERLOCK SWITCH
OC10		ROPE SAFETY SWITCH
OC11		LIGHT CURTAIN

AIR HANDLING

AH1		FAN
AH2		MANUAL DAMPER
AH3		DAMPER WITH OPERATOR
AH4		DAMPER SWING VALVE

WEB CONTROL

WC1		LOAD CELL
WC2		CENTER GUIDE
WC3		EDGE GUIDE
WC4		FULL WIDTH SPREADER
WC5		EDGE SPREADER
WC6		STATIC ELIMINATOR WITH IONIZED AIR
WC7		AMPLIFIER

THERMAL DEVICES

TD1		BURNER
TD2		TRANSFORMER
TD3		FLAME ROD
TD4		RHEOSTAT
TD5		RESISTANCE HEATER
TD6		HEAT EXCHANGER
TD7		HEAT TRANSFER CABLE

MISCELLANEOUS

M1		SEE NOTE
M2		SPECIAL DEVICE
M3		OPERATORS PANEL
M4		VARIABLE SPEED DRIVE
M5		PROGRAMMABLE LOGIC CONTROLLER
M6		WEIGHT
M7		VARIABLE FREQUENCY DRIVE

REVISIONS




Hot Melt Prepreg
By LITZLER

LITZLER
AUTOMATION
DRIVES & CONTROLS

PSC
AUDIO FREQUENCY BY LITZLER

THIS DRAWING IS THE PROPERTY OF C. A. LITZLER CO., INC. AND IS LOANED SUBJECT TO RETURN UPON DEMAND. BORROWER AGREES THAT SAME WILL NOT BE USED IN ANY WAY DETRIMENTAL TO OWNER'S INTEREST.

C. A. LITZLER CO., INC. ASSUMES NO RESPONSIBILITY, EITHER DIRECT OR INDIRECT, FOR ANY CHANGES IN ENGINEERING DESIGN, COMPLETENESS OF DESIGN, SUBSTITUTION OF MATERIALS OR SUBSTITUTION OR ALTERATION OF COMMERCIALY SUPPLIED OR FABRICATED COMPONENTS NOT IN COMPLETE UNIFORMITY WITH ITS DRAWINGS AND INSTRUCTIONS, UNLESS SUCH DESIGN CHANGES, DELETIONS, SUBSTITUTIONS OR ALTERATIONS ARE FIRST APPROVED BY C. A. LITZLER CO., INC. IN WRITING.

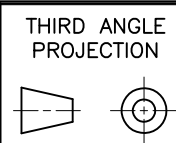

BREAK ALL SHARP
EDGES AND CORNERS
REMOVE ALL MACHINING
BURRS

UNLESS OTHERWISE SPECIFIED	
ALL DUAL DIMENSIONS ARE EXPRESSED INCHES/MILLIMETERS	
ALLOWABLE VARIATIONS:	
ENGLISH UNITS	METRIC UNITS
FRACTIONS: $\pm 1/16"$	NO DECIMALS: $\pm 1.5\text{mm}$
DECIMALS: $\pm 0.02"$	DECIMALS: $\pm 0.5\text{mm}$
$\pm 0.005"$	$\pm 0.1\text{mm}$
ANGLES: $\pm 0^\circ - 30'$	
ON METRIC ASSEMBLY DRAWINGS ROUND DECIMAL DIMENSIONS TO THE NEAREST WHOLE MILLIMETER.	

DRAWING APPROVAL

☐ APPROVED AS DRAWN ☐ APPROVED AS NOTED

NAME _____ DATE _____

C. A. LITZLER CO., INC.

CLEVELAND, OHIO 44135-2689, U.S.A. 216-267-8020 (FAX) 216-267-9856 WEBSITE: WWW.CALITZLER.COM

TITLE	DESIGN INFORMATION DOCUMENT	DRAWN BY	JLC	12/9/25
		CHECKED BY		
FOR	WINDER ACCUMULATOR A1/AK	APPROVED BY		
		APPROVED BY		

JOB NUMBER: 2058	SECTION: 98.24
------------------	----------------


SCALE: FULL SIZE

DWG. NO.	DID2058	02	A
		SHT.	R
TOTAL DRAWING SHEETS		3	

REF. DWG.

01.0 WINDER ACCUMULATOR AJ/AK

- 01.01 DANCER STYLE ACCUMULATOR, CONTROL POSITION OF THE ROLL TO CONTROL WEB TENSION
- 01.02 SOLENOID VALVE IS ENERGIZED TO CLOSE OUTFEED ROLL NIP, DE-ENERGIZE ON E-STOP (01-SV01)
- 01.03 WINDER ACCUMULATOR CONTROL PANEL WITH:
 - ACCUMULATOR OFF/ON SELECTOR SWITCH
 - LINE STOP PUSHBUTTON
 - E-STOP PUSHBUTTON
 - OUTFEED NIP AUTO/OPEN/CLOSE ILLUMINATED SELECTOR SWITCH
- 01.04 LOWER LIMIT SWITCH INDICATES ACCUMULATOR EMPTY AND STOPS WINDER (01-LS01)
- 01.05 UPPER LIMIT SWITCH INDICATES ACCUMULATOR FULL AND STOPS LINE (01-LS02)
- 01.06 LINEAR TRANSDUCER TO INDICATE THE CARRIAGE POSITION
FILL PRESSURE TO BE REGULATED BY CARRIAGE POSITION
- 01.07 I/P TO CONTROL TENSION
- 01.08 LOAD CELLS FOR TENSION CONTROL (01-LC01)
 - TWO (2) LOAD CELLS TS-150-FC
 - CONNECT TO COMMON AMPLIFIER
- 01.09 STORAGE IS 26 SECONDS AT 23 FPM
- 01.10 I/P COUNTER PRESSURE USED TO SMOOTH START OF CARRIAGE TRAVEL
- 01.11 ONE-WAY CLUTCH
- 01.12 SINGLE SOLENOID VALVE IS ENERGIZED TO PRESSURIZE CARRIAGE LIFT CYLINDERS (01-SV02)
- 01.13 SIX (6) IDLER ROLLS. DEADSHAFT (ONE LOCATED ON THE PLATFORM)
 - SIZE: 4" DIA. X 67" ROLL FACE
 - MATERIAL: ALUMINUM ANODIZED BLACK
- 01.14 NIP ROLL
 - UPPER ROLL ø5 1/2" WITH 9/16" HYPALON (OR EQUAL) 75 SHORE A DUROMETER
 - LOWER ROLL ø5 1/2" STEEL CHROME PLATED
 - ROLL FACE 67"
- 01.15 TWO (2) AIR CYLINDERS 3 1/4" BORE X 32 1/2" STROKE FOR CARRIAGE MOVEMENT
- 01.16 TWO (2) AIR CYLINDERS 3 1/4" BORE X 3" STROKE FOR NIP
- 01.17 ENCODER FIELD MOUNTED ON EXISTING TURRET WINDER

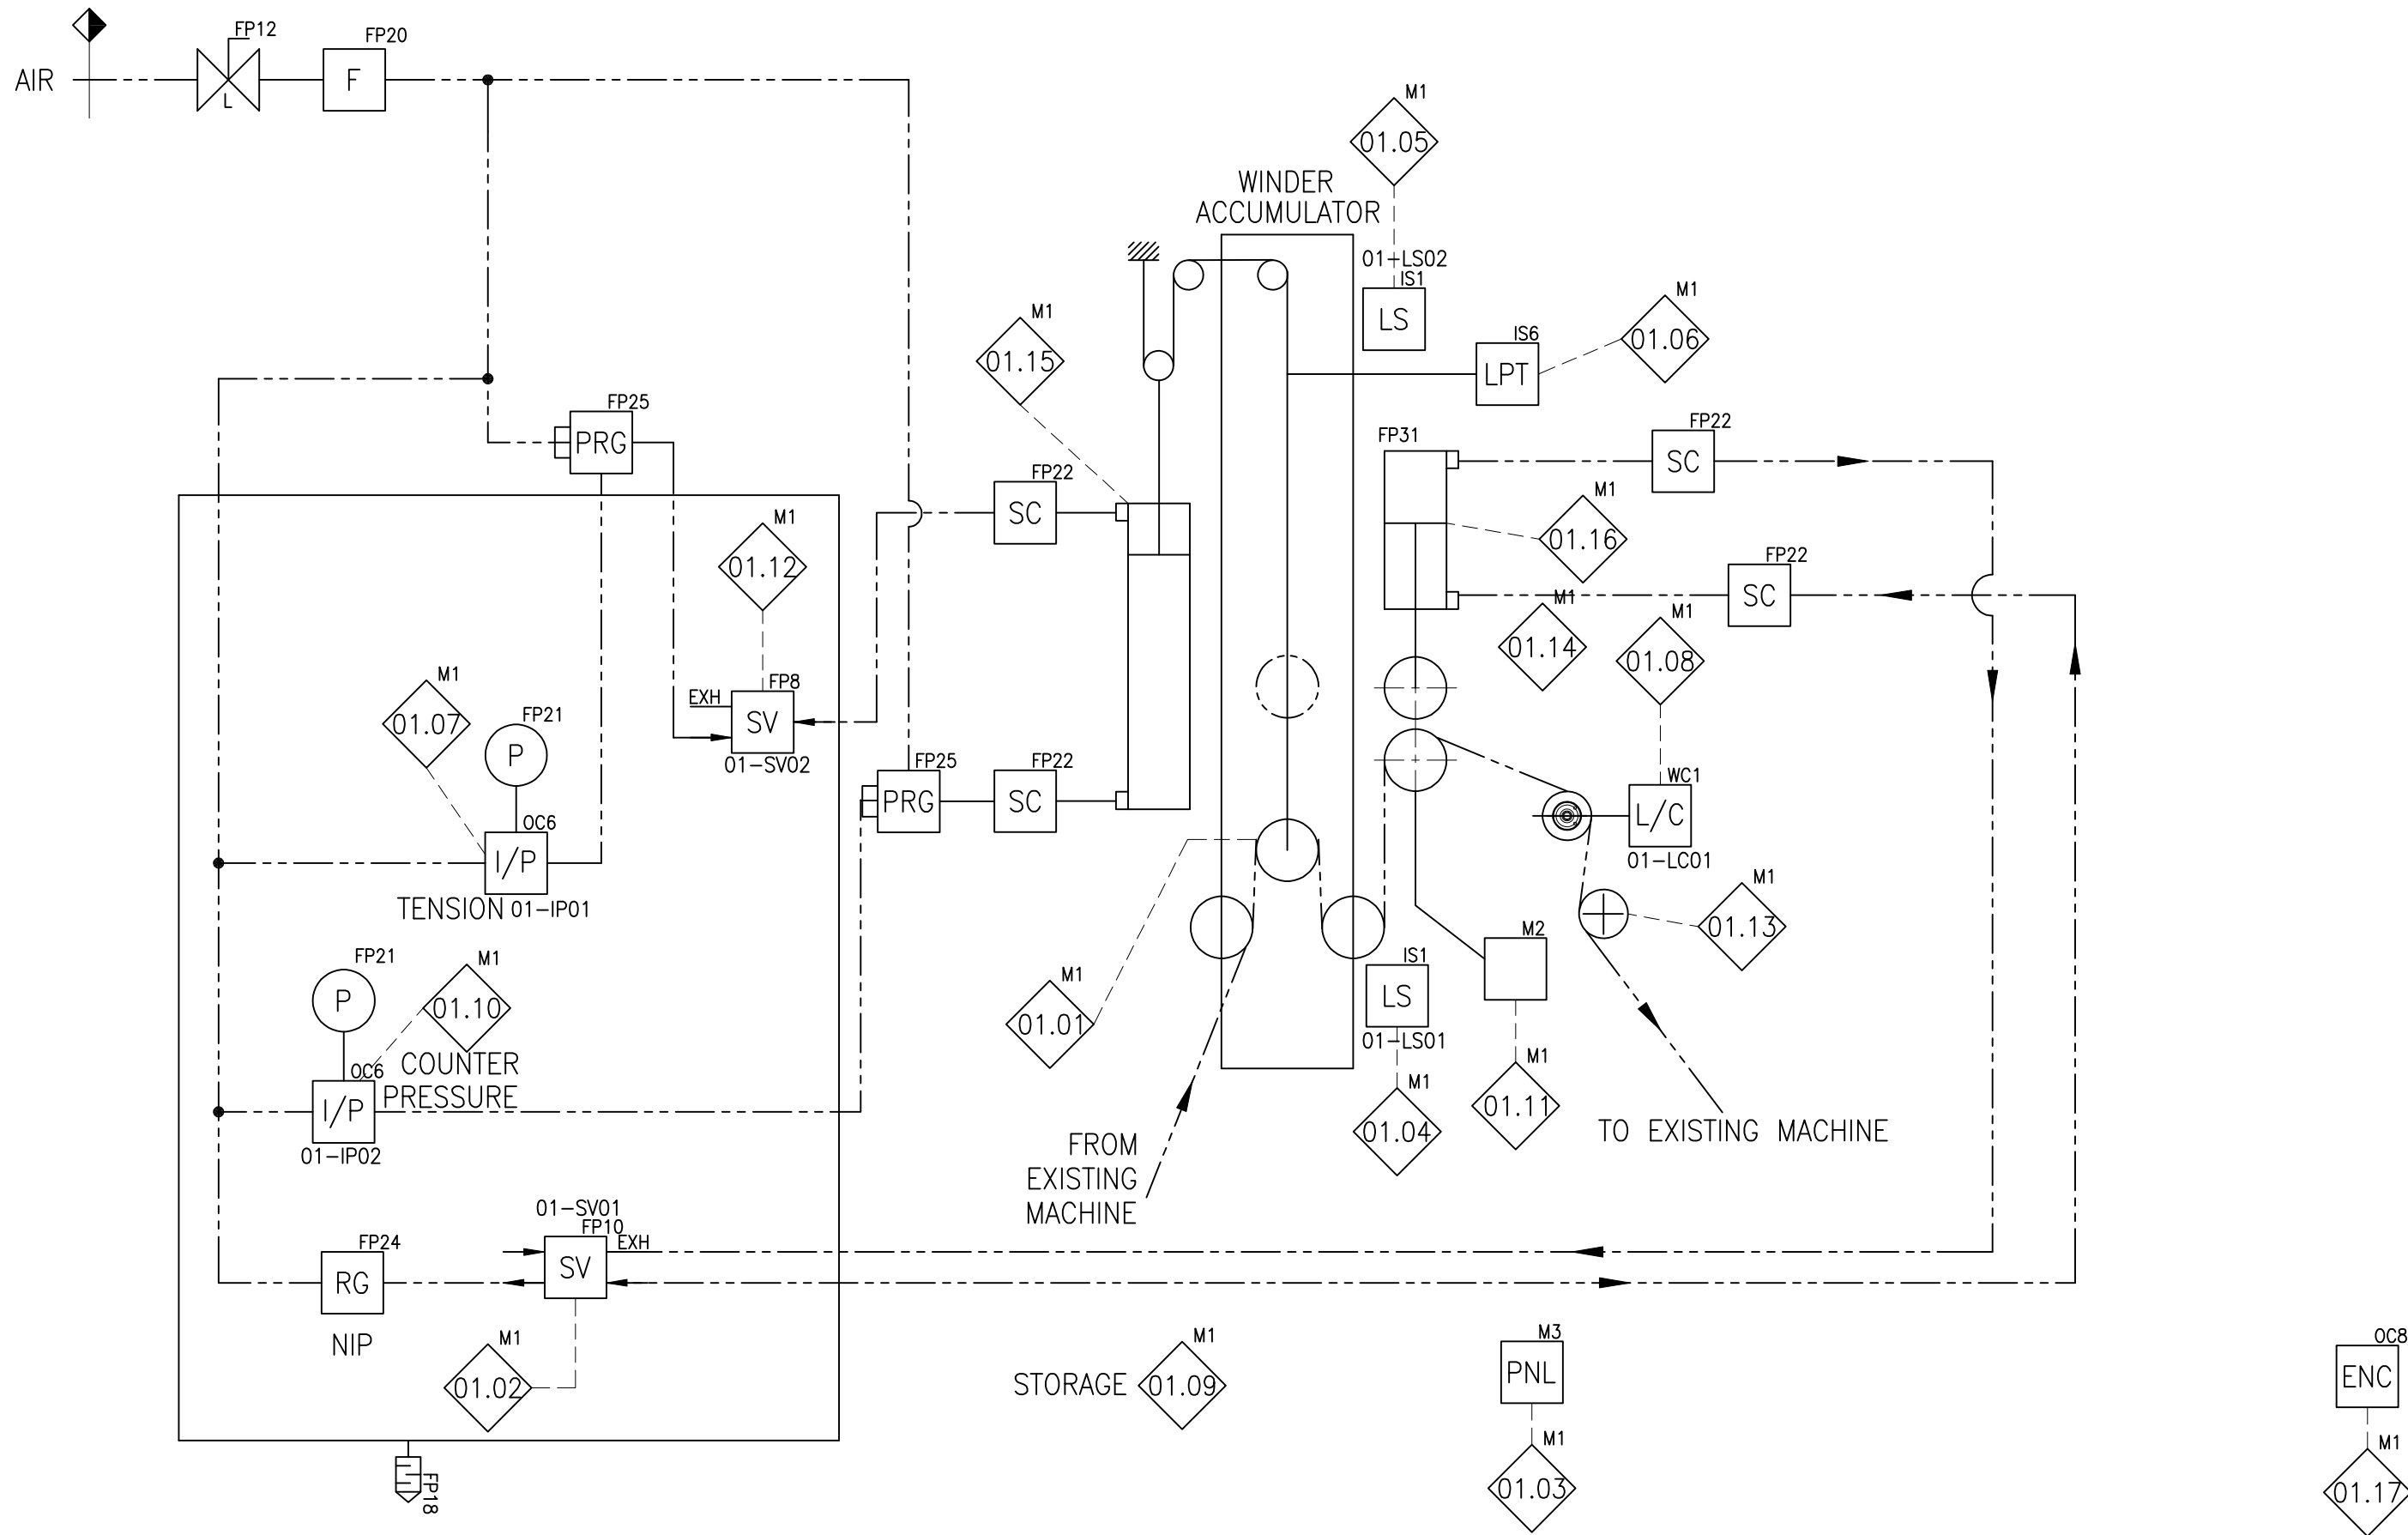

NOTE:
THE FOLLOWING DENOTES SCOPE
OF SUPPLY:
BY LITZLER
BY OTHERS

REVISIONS	WAE CO. Hot Mail Printing By LITZLER			LITZLER AUTOMATION DRIVES & CONTROLS		PSC RADIO FREQUENCY BY LITZLER		THIS DRAWING IS THE PROPERTY OF C. A. LITZLER CO., INC. AND IS LOANED SUBJECT TO RETURN UPON DEMAND. BORROWER AGREES THAT SAME WILL NOT BE USED IN ANY WAY DETRIMENTAL TO OWNER'S INTEREST.		THIRD ANGLE PROJECTION 		UNLESS OTHERWISE SPECIFIED ALL DUAL DIMENSIONS ARE EXPRESSED IN INCHES/MILLIMETERS ALLOWABLE VARIATIONS: <table><tr><th>ENGLISH UNITS</th><th>METRIC UNITS</th></tr><tr><td>FRACTIONS: ±1/16"</td><td>NO DECIMALS ±1.5mm</td></tr><tr><td>DECIMALS: .XX ± .005</td><td>DECIMALS: .X ± .05mm</td></tr><tr><td>XX ± .005"</td><td>XX ± .05mm</td></tr></table>		ENGLISH UNITS	METRIC UNITS	FRACTIONS: ±1/16"	NO DECIMALS ±1.5mm	DECIMALS: .XX ± .005	DECIMALS: .X ± .05mm	XX ± .005"	XX ± .05mm	DRAWING APPROVAL ☐ APPROVED AS DRAWN ☐ APPROVED AS NOTED		C. A. LITZLER CO., INC. CLEVELAND, OHIO 44135-2689, U.S.A. 216-267-8020 (FAX) 216-267-9856 WEBSITE: WWW.CALITZLER.COM				JOB NUMBER: 2058 SECTION: 98.24	
	ENGLISH UNITS	METRIC UNITS																											
	FRACTIONS: ±1/16"	NO DECIMALS ±1.5mm																											
	DECIMALS: .XX ± .005	DECIMALS: .X ± .05mm																											
	XX ± .005"	XX ± .05mm																											
C. A. LITZLER CO., INC. ASSUMES NO RESPONSIBILITY, EITHER DIRECT OR INDIRECT, FOR ANY CHANGES IN ENGINEERING DESIGN, COMPLETENESS OF DESIGN, SUBSTITUTION OF MATERIALS OR SUBSTITUTION OR ALTERATION OF COMMERCIALLY SUPPLIED OR FABRICATED COMPONENTS NOT IN COMPLETE UNIFORMITY WITH ITS DRAWINGS AND INSTRUCTIONS, UNLESS SUCH DESIGN CHANGES, OMISSIONS, SUBSTITUTIONS OR ALTERATIONS ARE FIRST APPROVED BY C. A. LITZLER CO., INC. IN WRITING.								BREAK ALL SHARP EDGES AND CORNERS REMOVE ALL MACHINING BURRS		ON METRIC ASSEMBLY DRAWINGS ROUND DECIMAL DIMENSIONS TO THE NEAREST WHOLE MILLIMETER		NAME _____ DATE _____		TITLE DESIGN INFORMATION DOCUMENT		DWG. NO. DID2058 03 A													
M&CT MOLDING & COATING TECHNOLOGIES			Quickdraft® Computerized Drafting Systems By LITZLER										FOR WINDER ACCUMULATORS AJ/AK		APPROVED BY		SHT. REV.												
													APPROVED BY		TOTAL DRAWING SHEETS 3														